

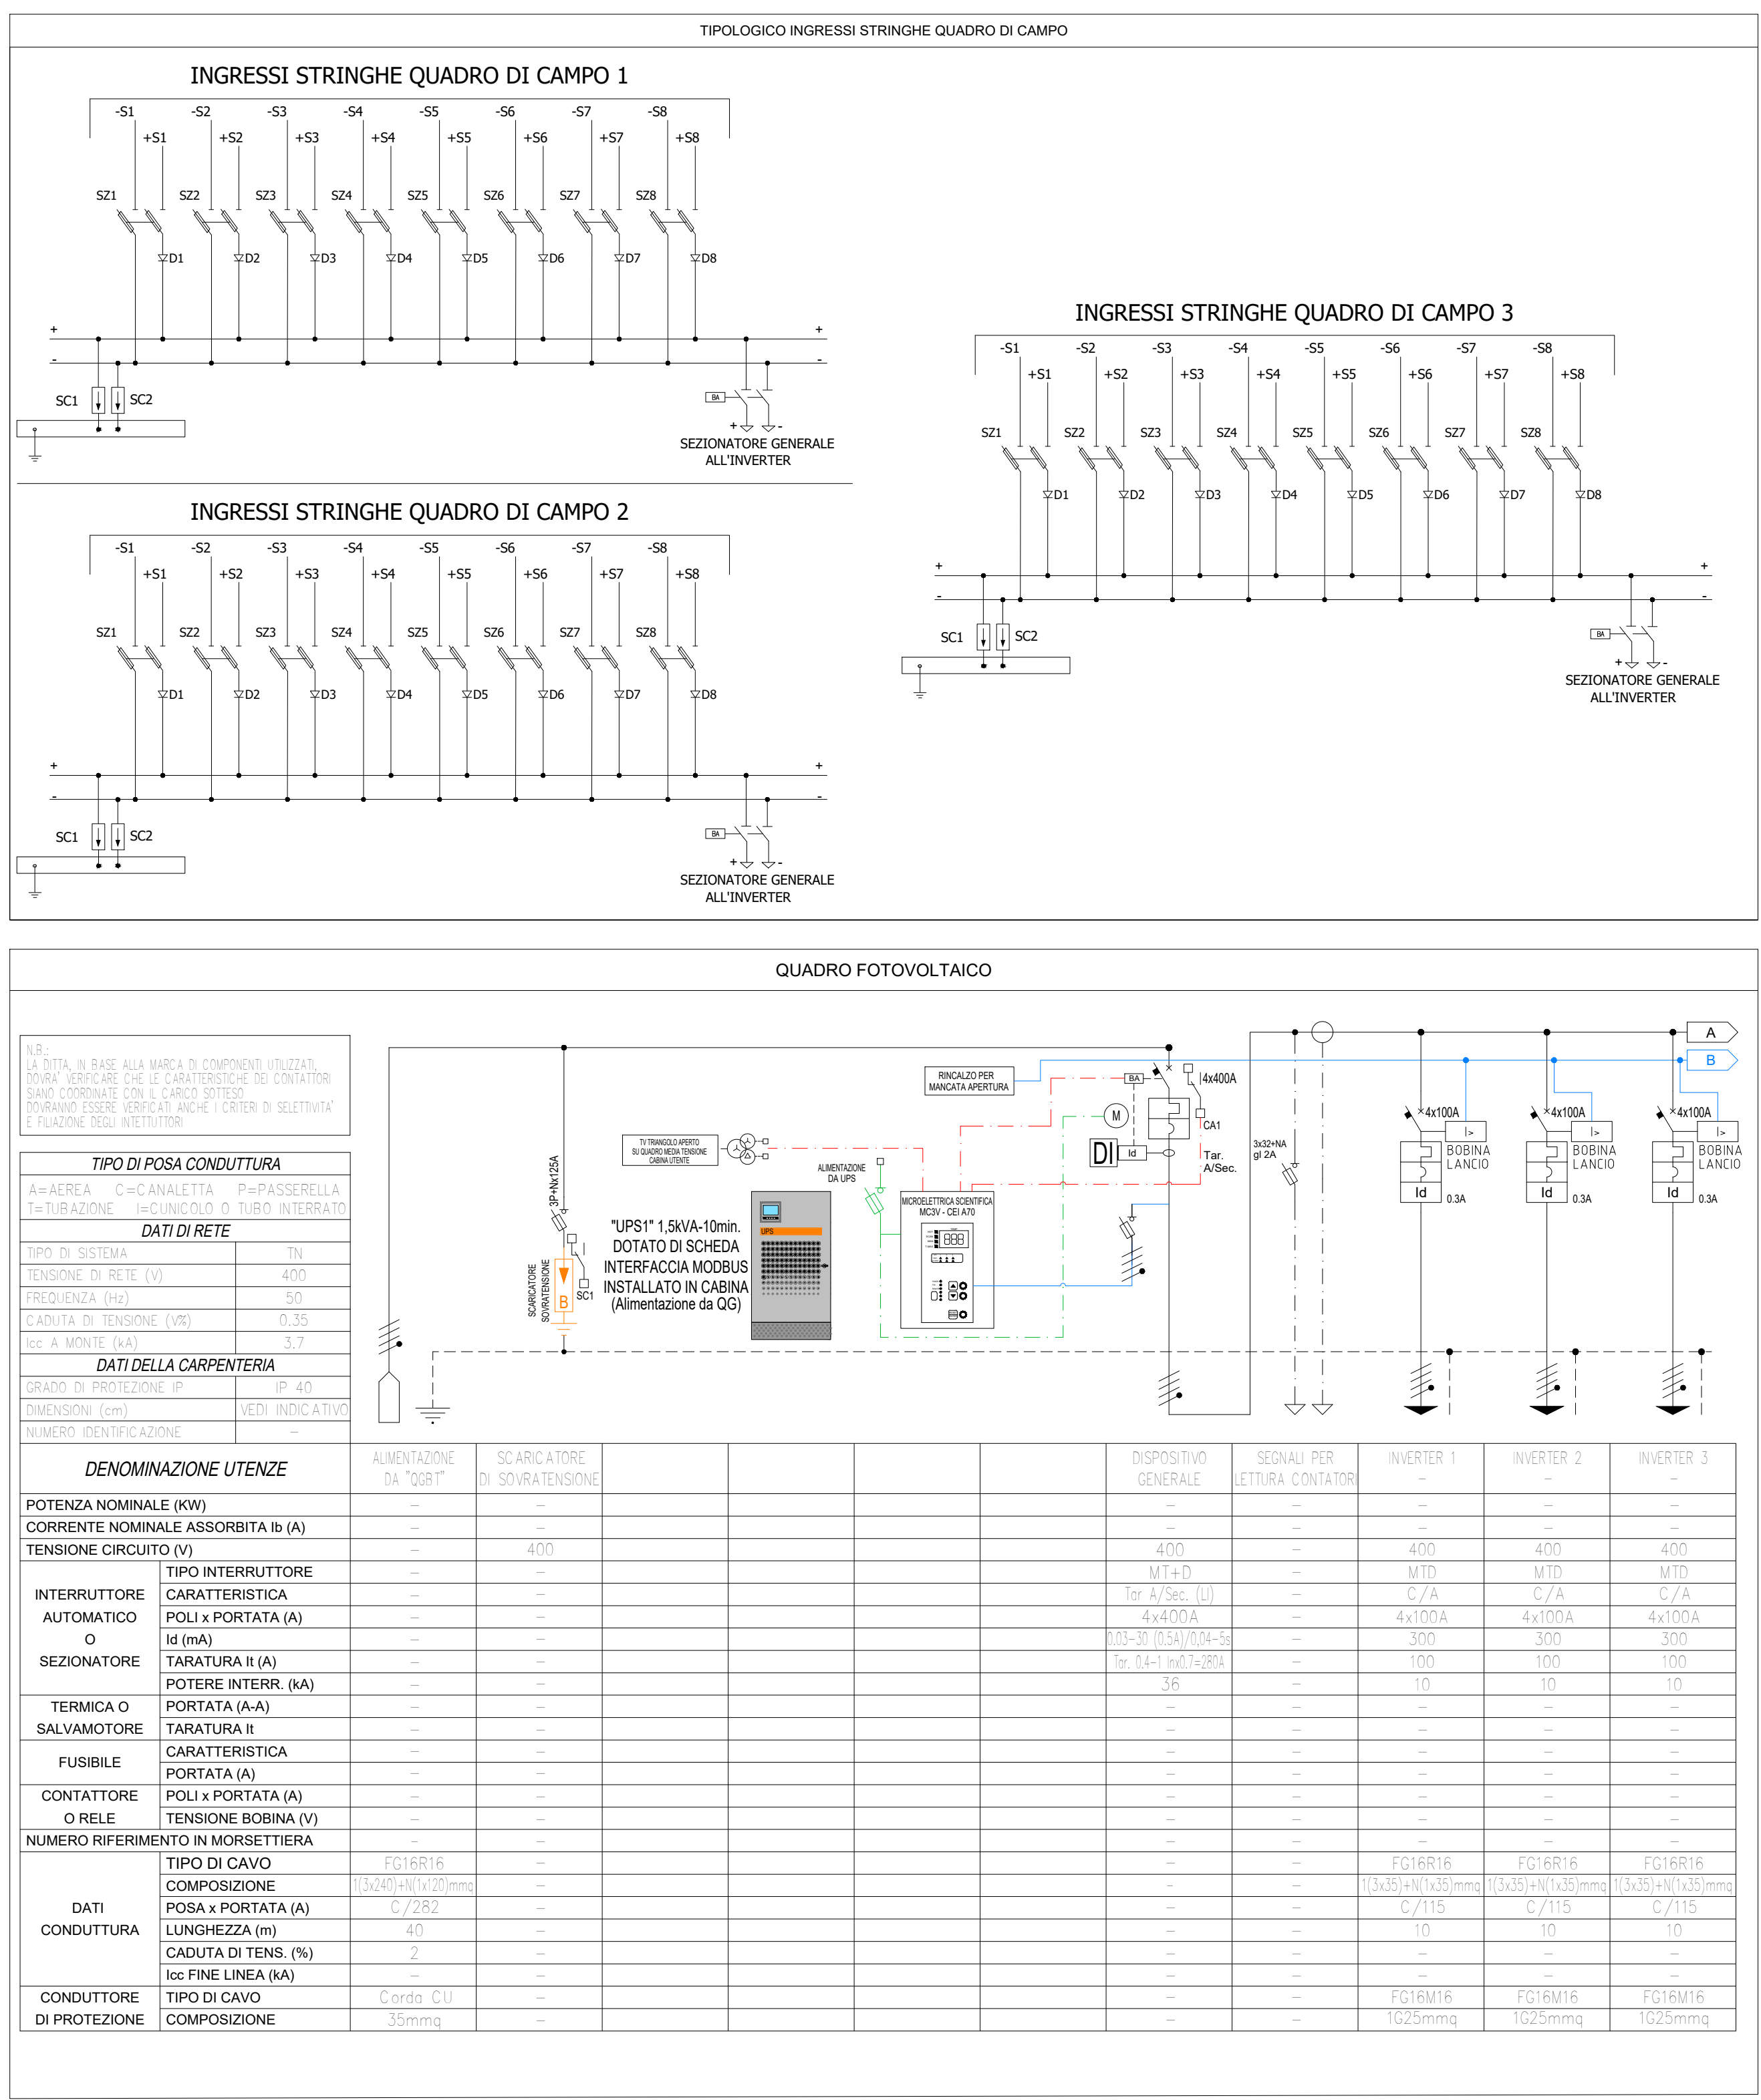


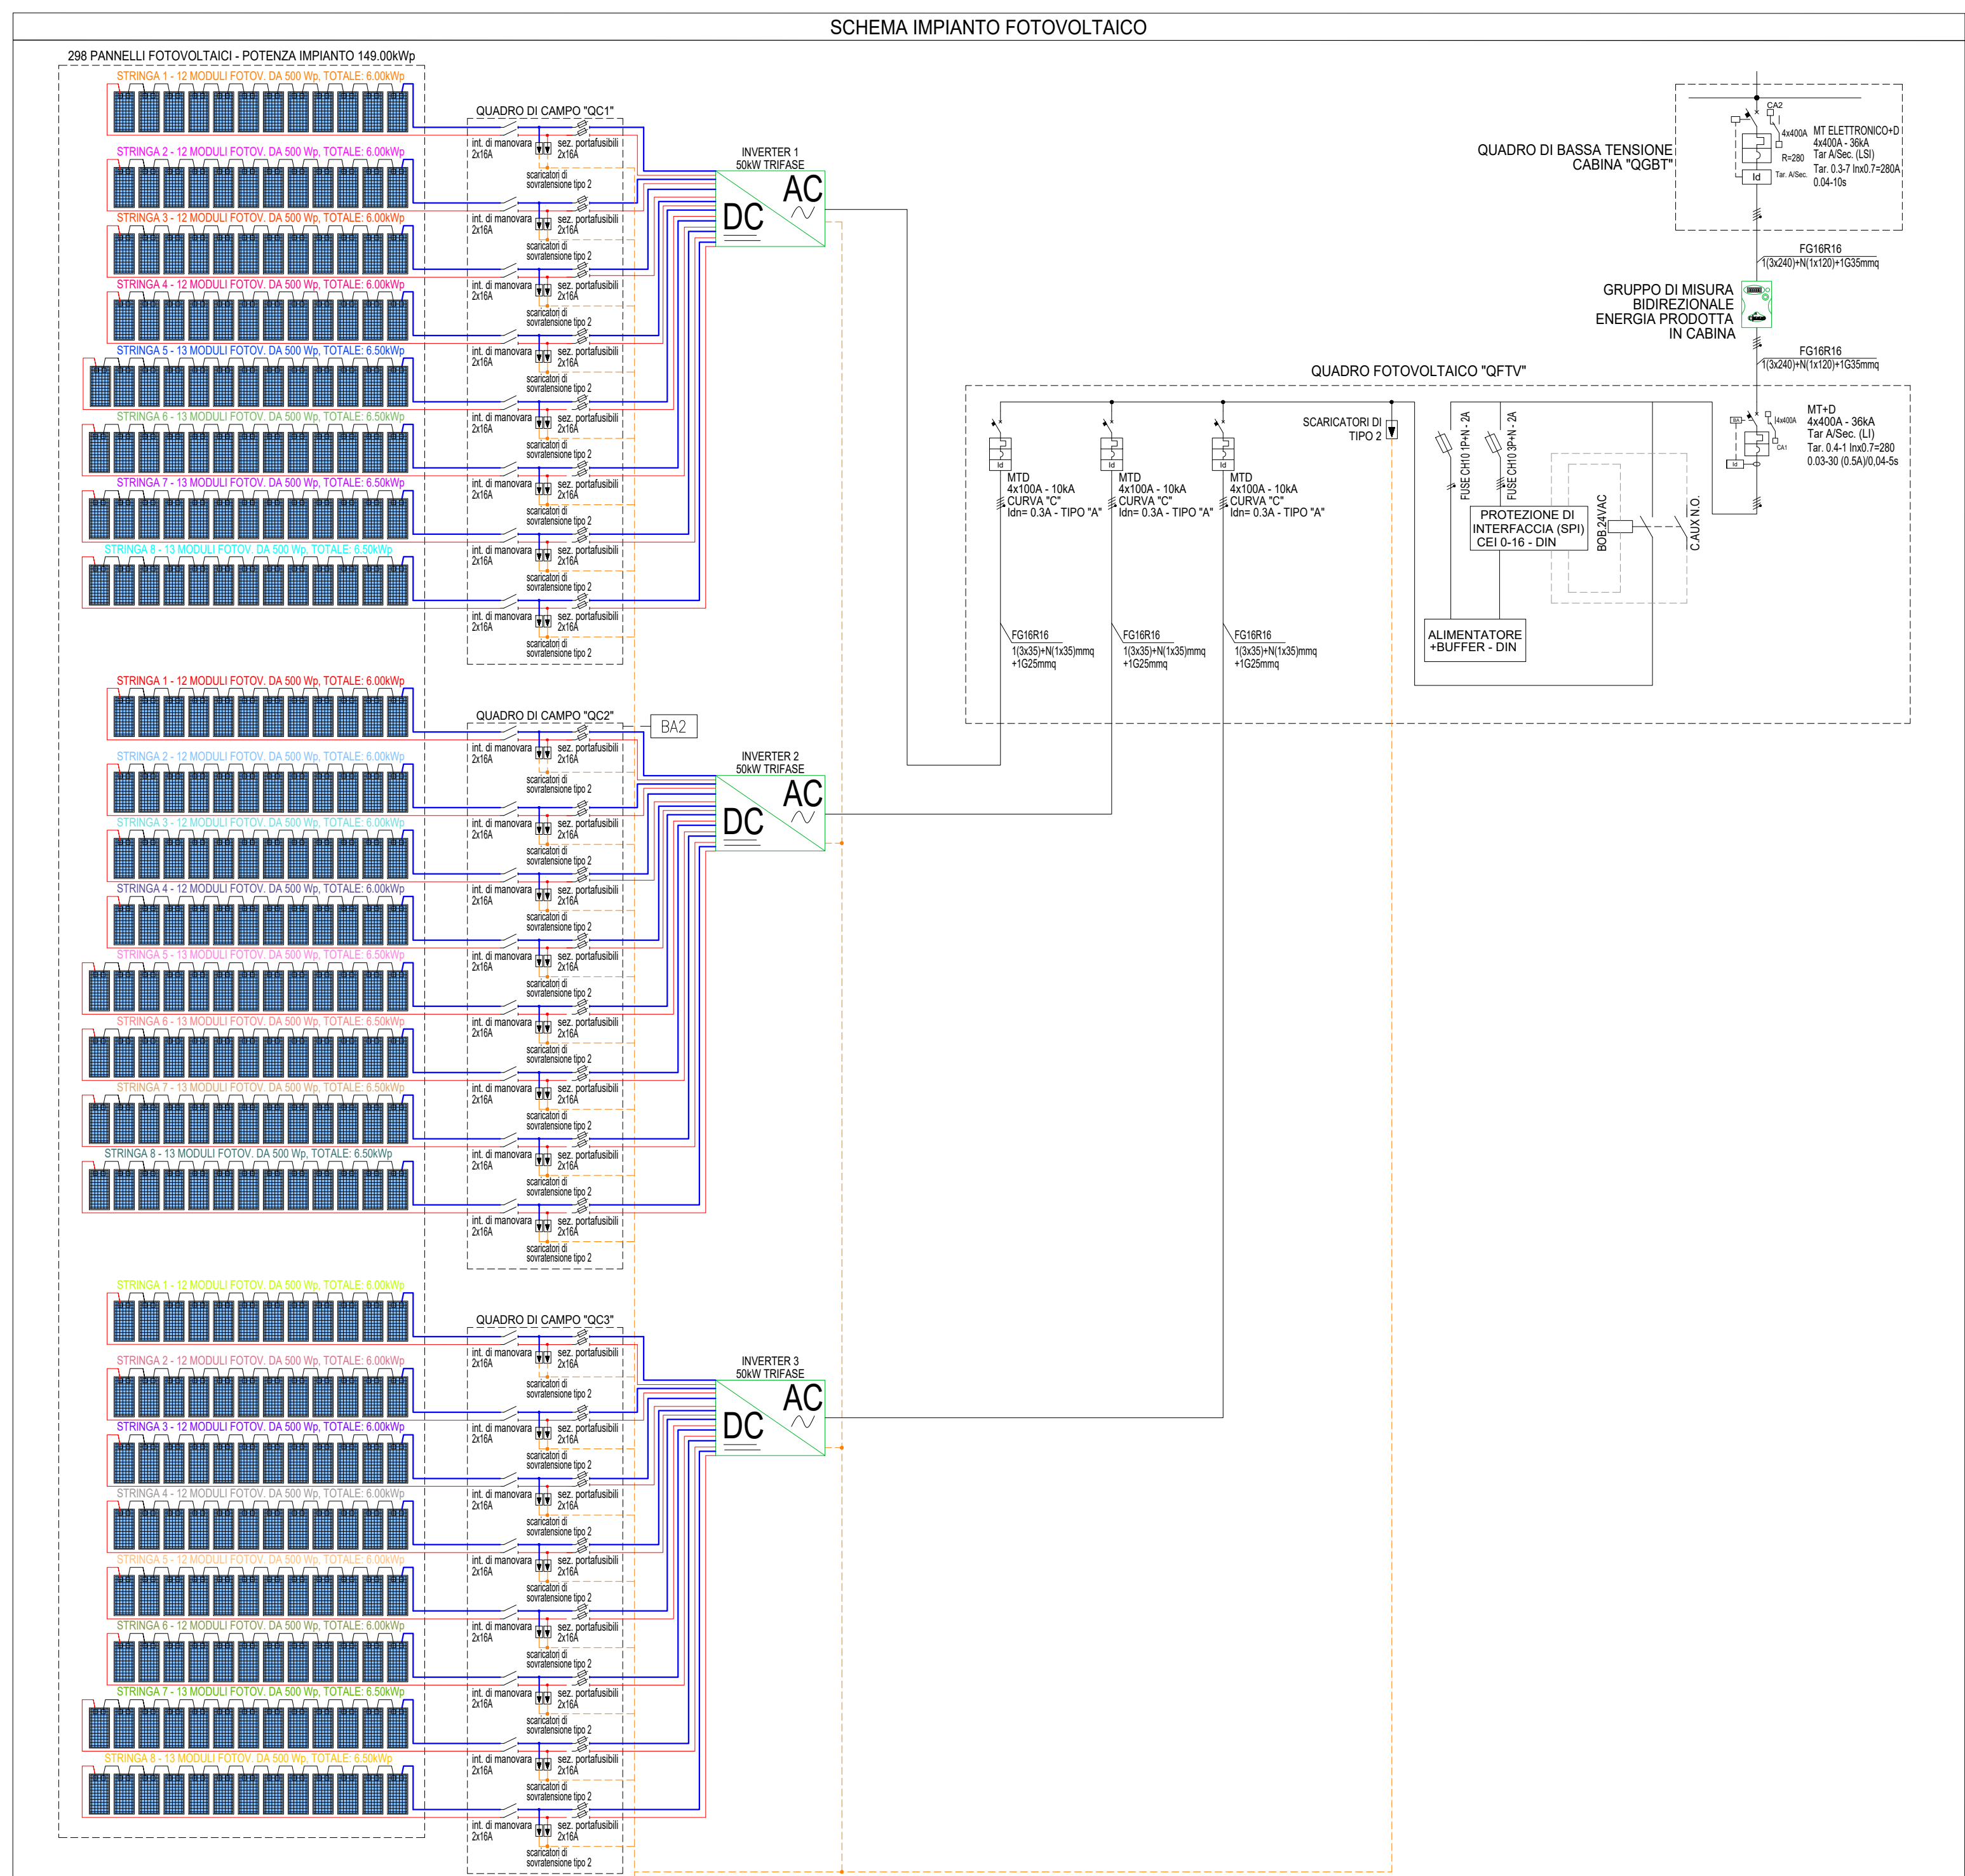

LEGENDA SIMBOLI

	QUADRO ELETTRICO
	QUADRO IMPIANTO FOTOVOLTAICO
	QUADRO DI CAMPO
	INVERTER
	PANNELLO FOTOVOLTAICO IN SILICIO MONOCRISTALLINO 60Wp
	RIPARTIZIONE STRINGHE
	CANALE METALLICO DELLE DIMENSIONI INDICATE PER IMPIANTO DI FORZA MOTRICE
	UNITÀ CURVE ASCENDENTI/DISCENDENTI PER CANALINE METALLICHE ASSOLATE O CON COPERCHIO
	DERIVAZIONI A CROCE PER CANALINE METALLICHE ASSOLATE O CON COPERCHIO
	DERIVAZIONI A T PER CANALINE METALLICHE ASSOLATE O CON COPERCHIO
	CURVE PIANE PER CANALINE METALLICHE ASSOLATE O CON COPERCHIO
	CONDUITTURA ASCENDENTE

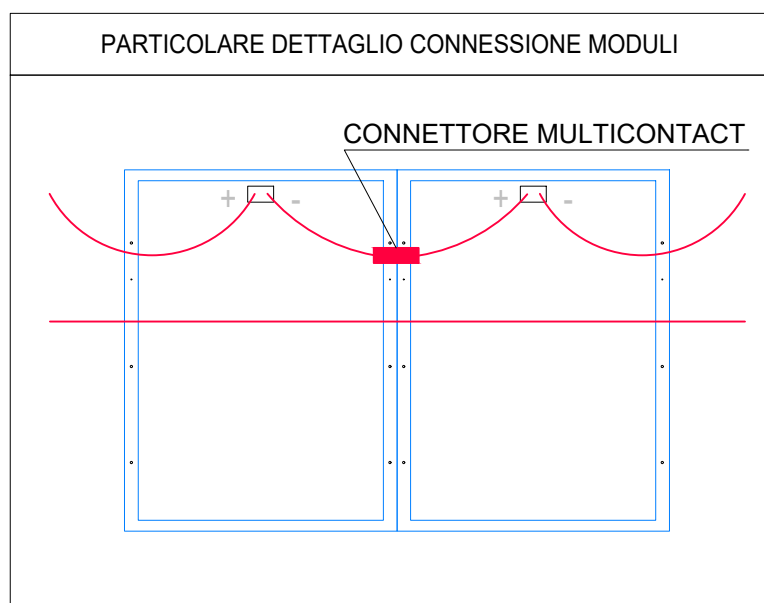

COMUNE DI POGGIBONSI
PROVINCIA DI SIENA

NUOVA SCUOLA "P. CALAMANDREI"
IN VIA ALDO MORO

PROGETTO ESECUTIVO

ATI DI PROGETTAZIONE:

MANDATARIA
EUTECNE
architettura | ingegneria

MANDANTI
SINERGIE
Via Roma, 30
51018 Poggibonsi
Tel. 0578 20 20 20
Fax 0578 20 20 20
www.sinergie.it

RESPONSABILE DELLA PROGETTAZIONE
ING. FEDERICO FRAPPI

GRUPPO DI PROGETTAZIONE
Dott. Arch. Pierpaolo PAPI
Dott. Ing. Luca DELL'AVVERSIANO
Dott. Ing. Martina RICCI
Ing. SARA ANTONELLI

MANDANTI
Dott. Arch. Olimpia LORENZINI
Dott. Arch. Luca FRAPPI
Dott. Arch. Debora PALUANO
Dott. Ing. Dario BIANCHI

COMITENTE
COMUNE DI POGGIBONSI
R.U.P. Arch. Vito Deabato

TITOLO	IMPIANTI ELETTRICI Impianto fotovoltaico	COMMESSA	ELABORATO	REVISIONE	
REV. N	DATA	MOTIVO DELLA EMISSIONE	ESEGUITO	CONTROLLATO	APPROVATO
A	APR 2021	PROGETTO ESECUTIVO	FARDINO	F. FRAPPI	F. FRAPPI
B	GEN 2024	PROGETTO ESECUTIVO - VERIFICA			