
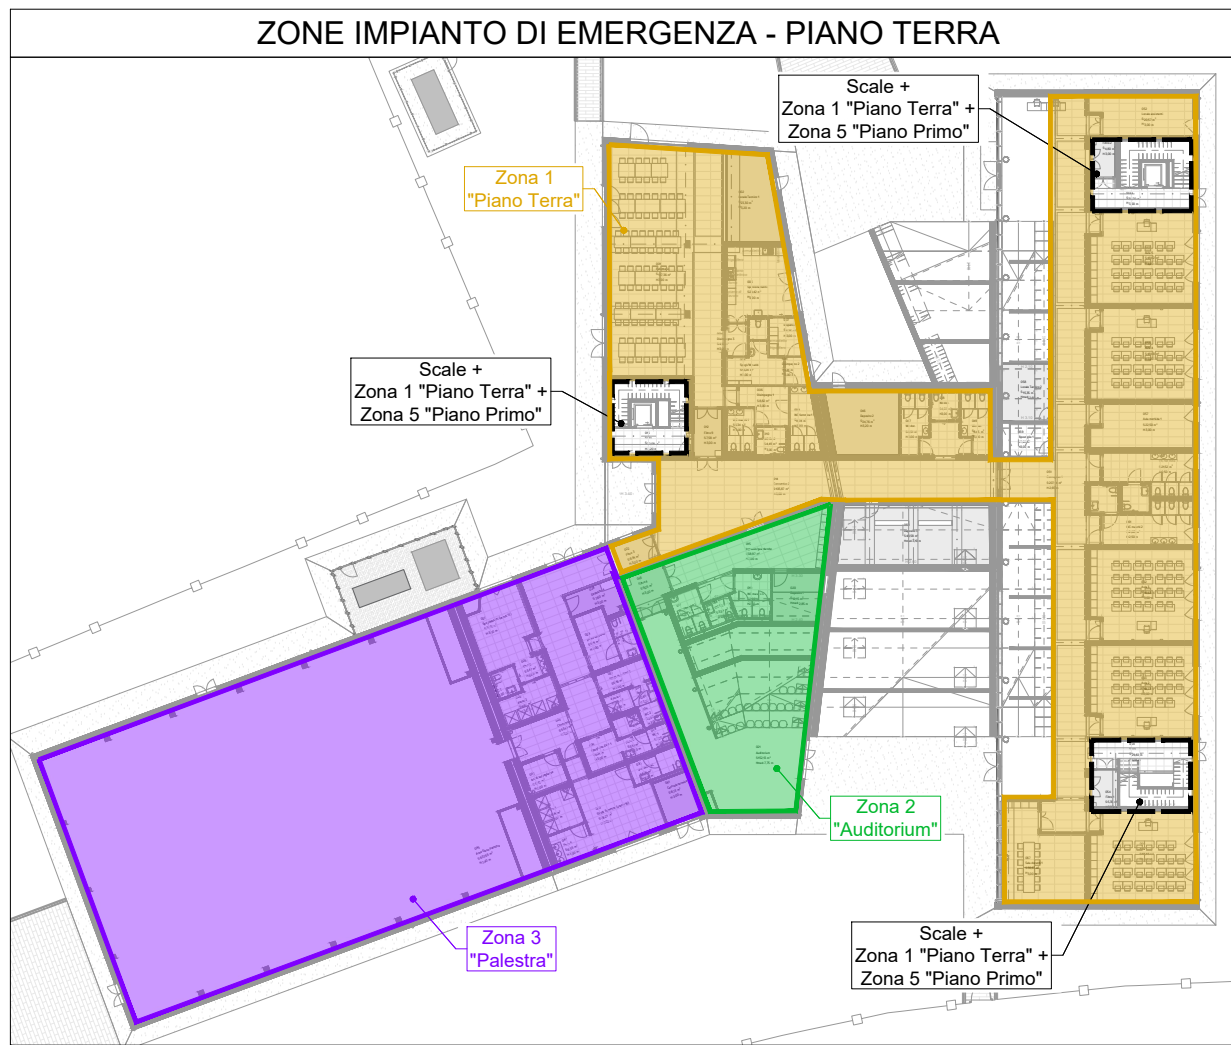
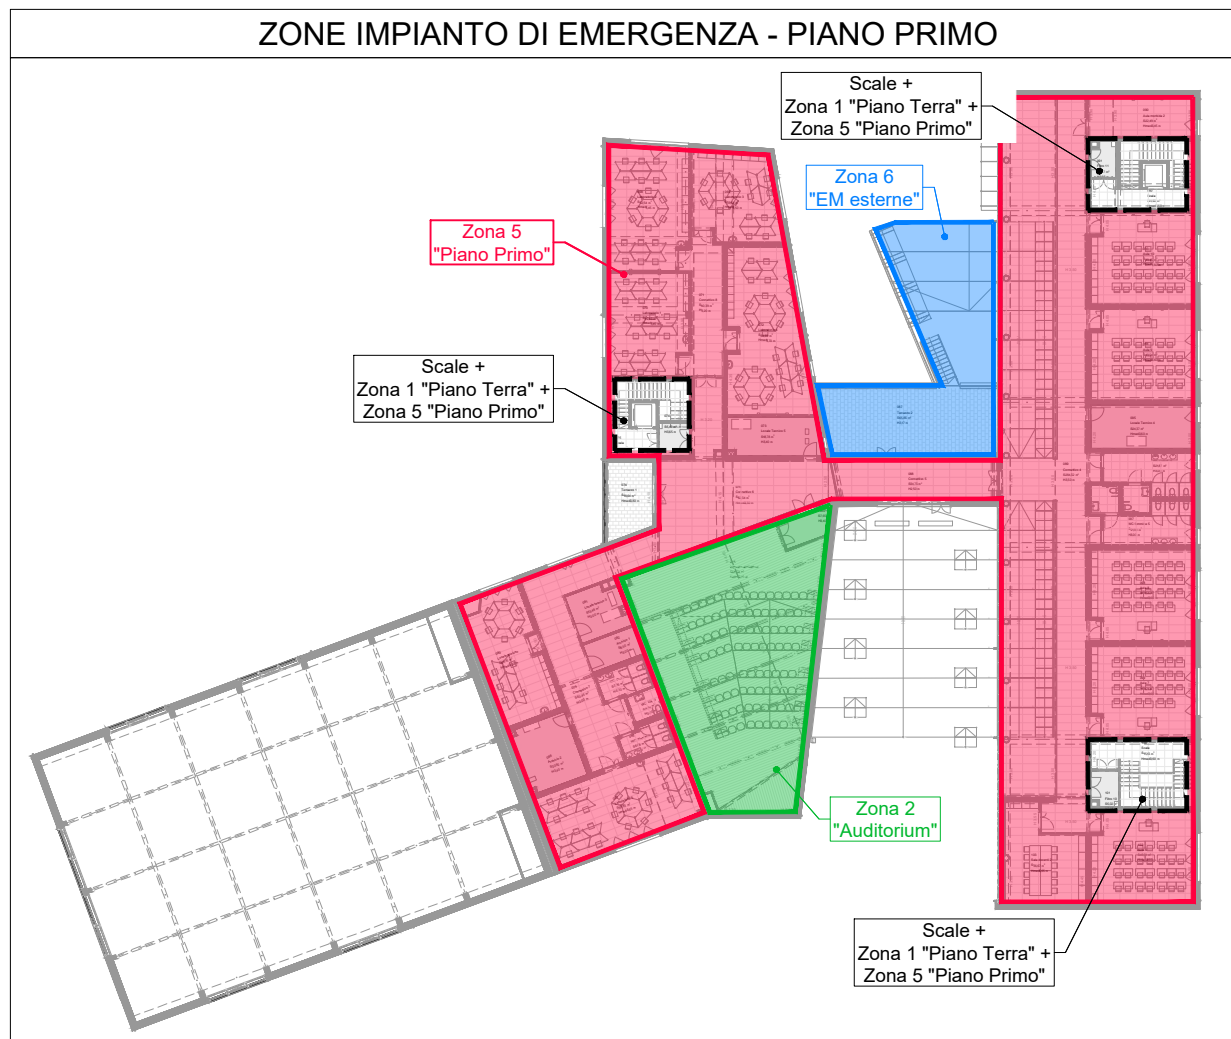
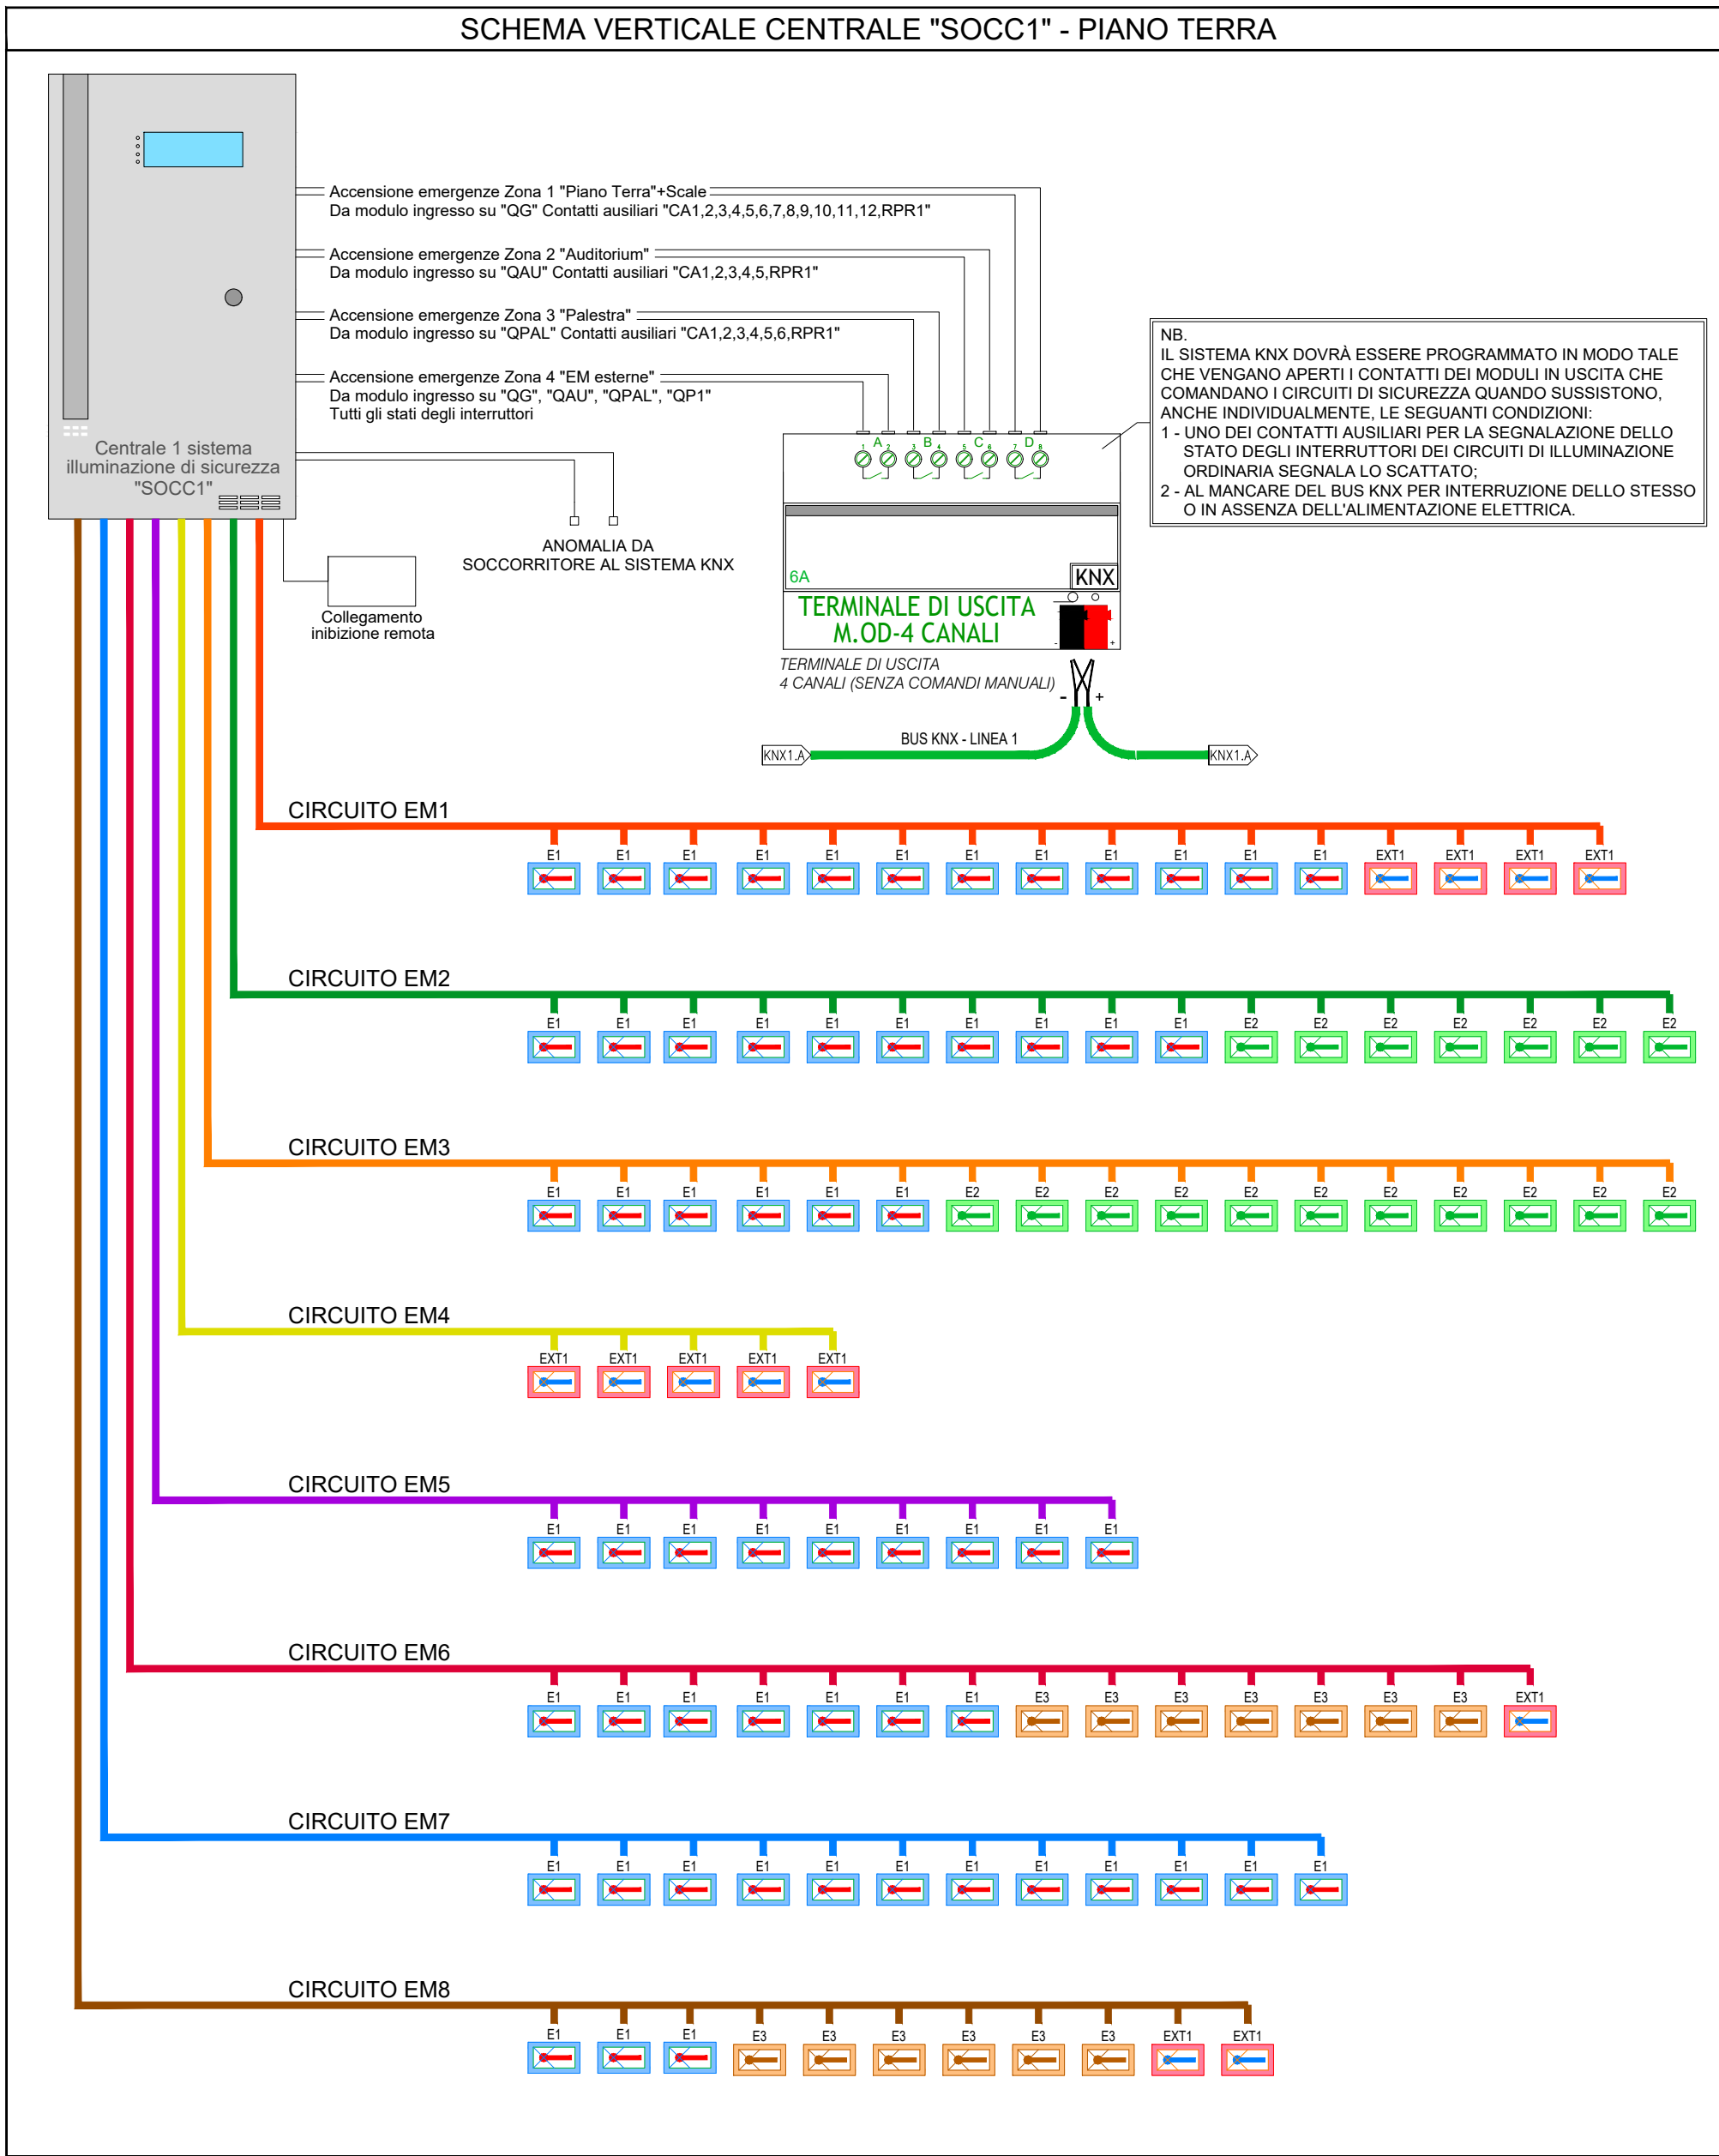


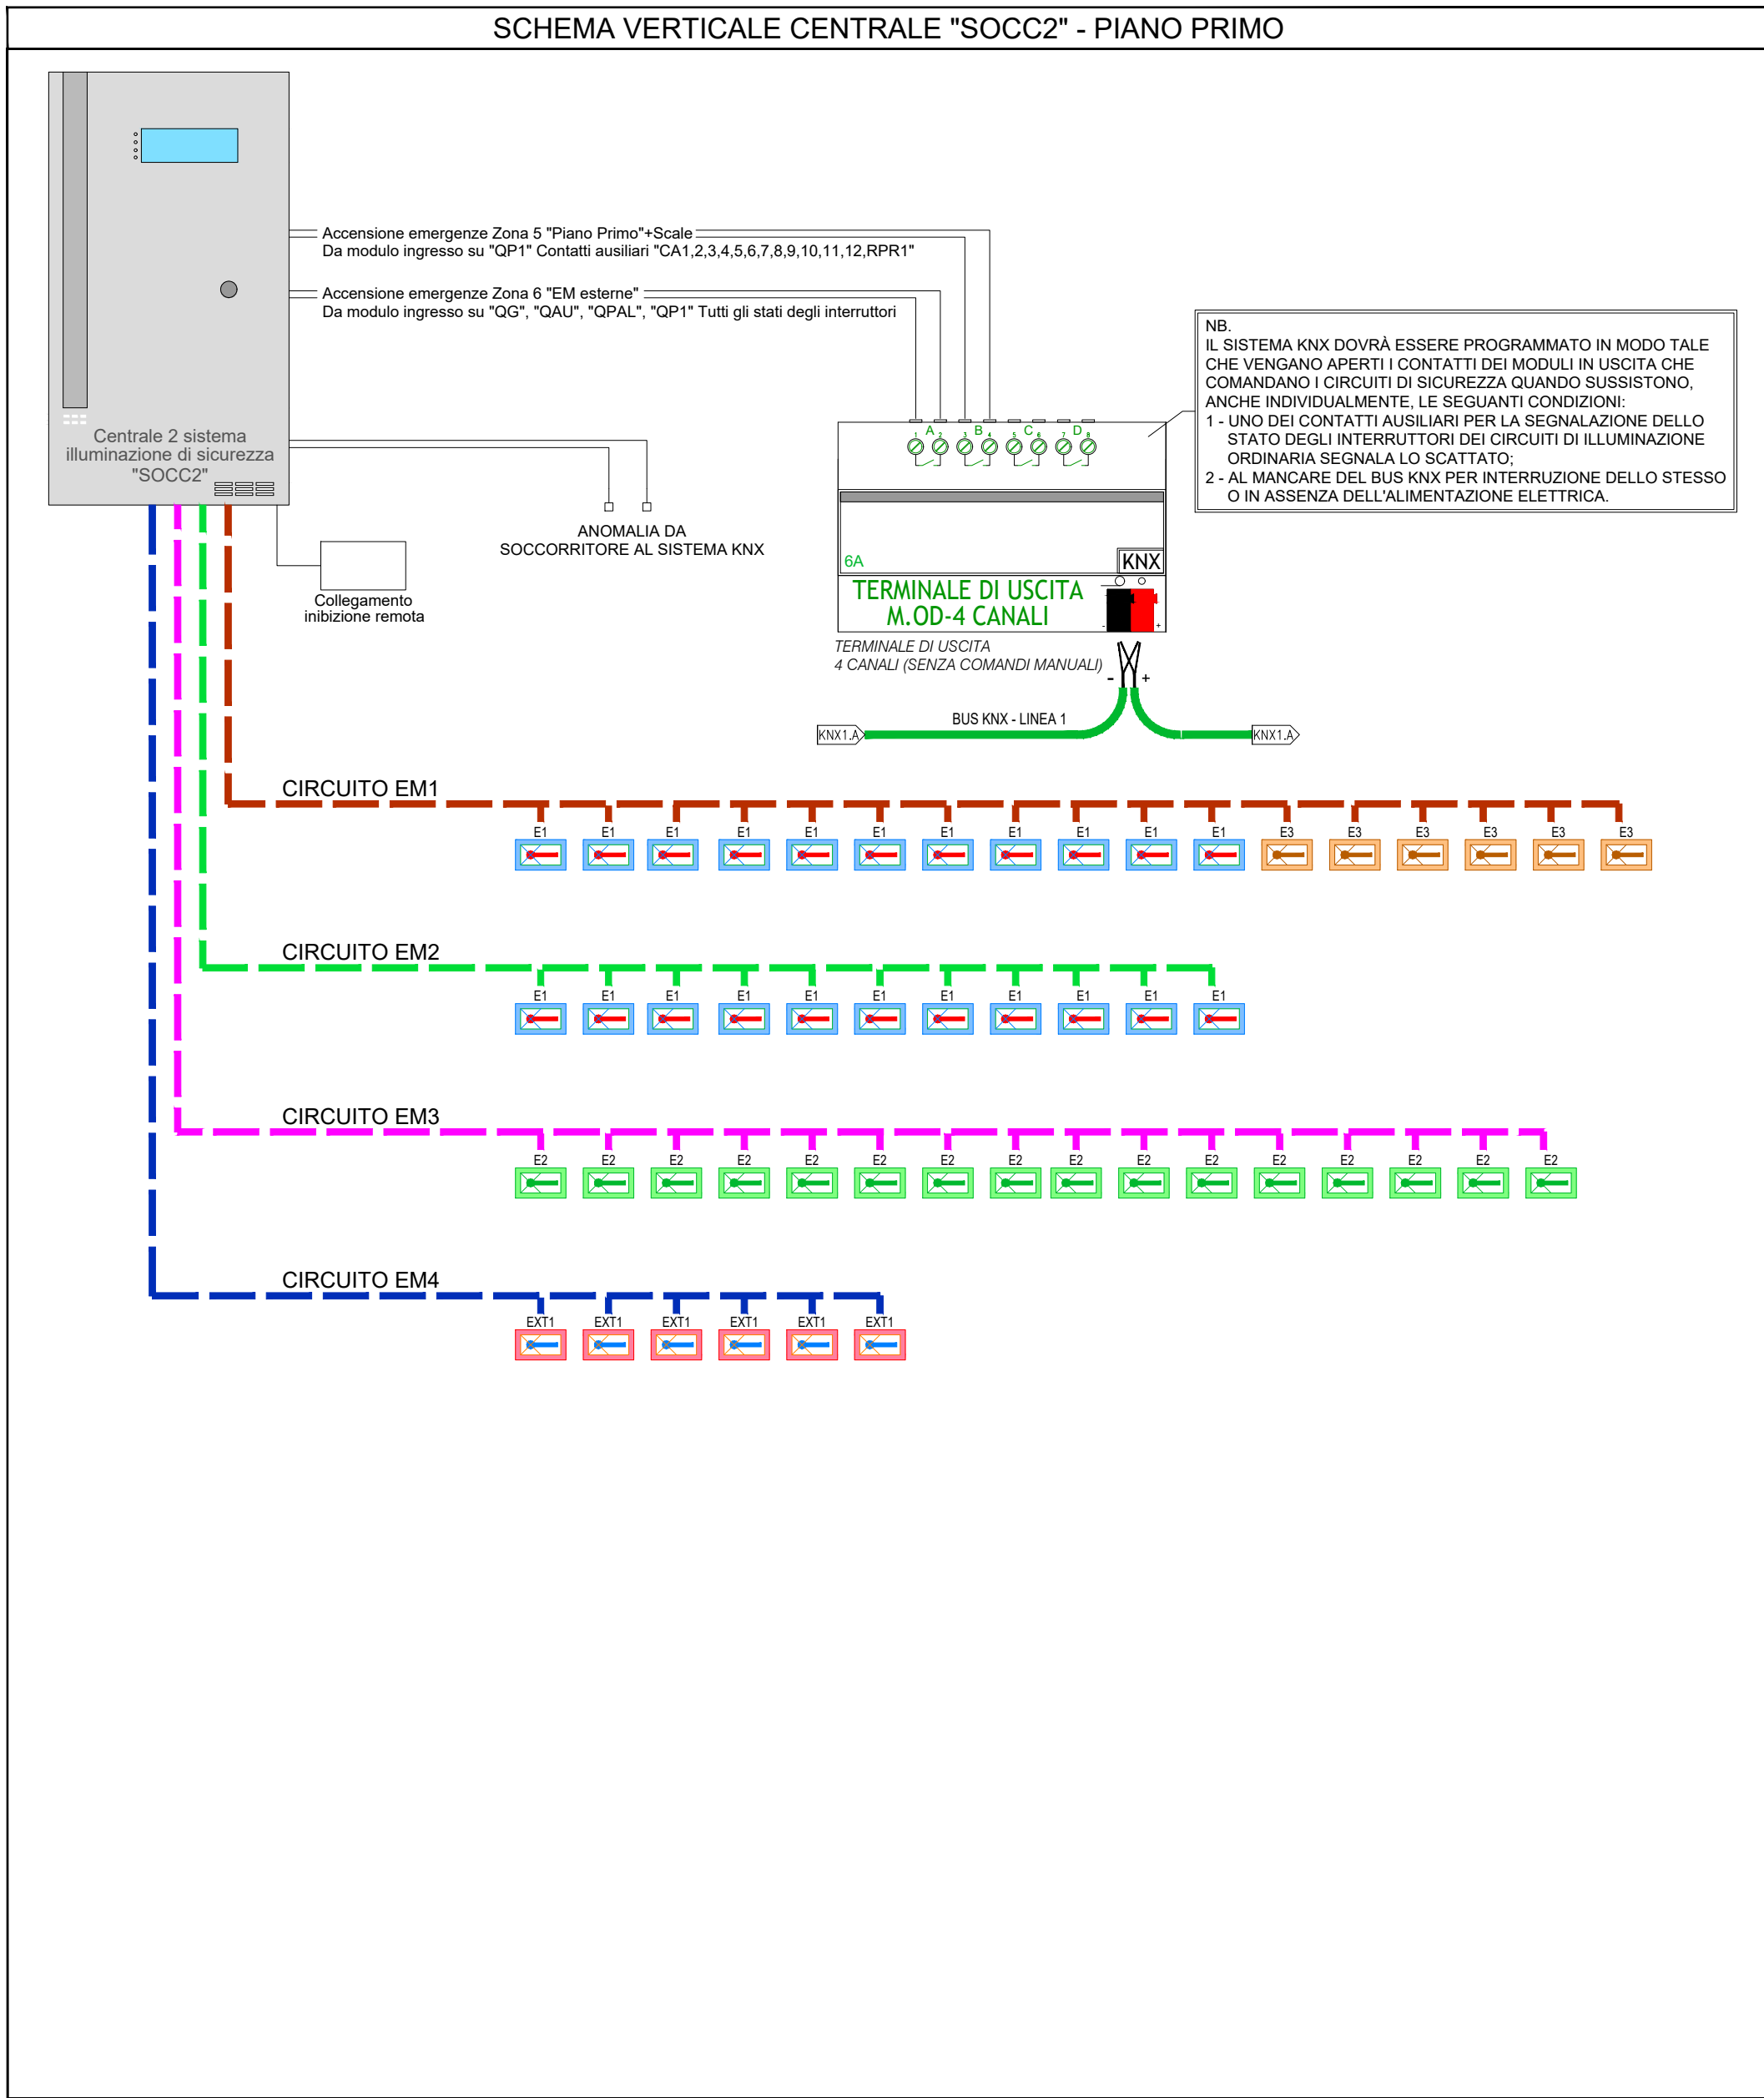

LEGENDA SIMBOLI

	QUADRO ELETTRICO
	RACK TRASMISSIONE DATI
	UPS
	CENTRALE ALLARME INCENDI E TERREMOTO
	CENTRALE TV SATELLITE
	SISTEMA CENTRALIZZATO IN BASSA TENSIONE 230V PER ALIMENTAZIONE E CONTROLLO DEGLI APPARECCHI DI EMERGENZA LED ALIMENTAZIONE 230V - TENSIONE IN USCITA 230V - IL LINE DI USCITA PER ALIMENTAZIONE E CONTROLLO DELLE LAMPADINE DI EMERGENZA 4 INGRESSI PROGRAMMABILI A TENSIONE DI RETE A 230 VAC UTILIZZABILI PER ATTIVAZIONE DI EMERGENZA LOCALE INGRESSI DIGITALI UTILIZZABILI COME SONAL E MODO PROGRAMMABILE CARGO MASSIMO PER CIRCUITO 80W - 20 LAMPADINE AUTONOMA 1h - 480W MARCA "ENERGY" MODELLO "SPR CENTER 10" CODICE SC2004
	SISTEMA CENTRALIZZATO IN BASSA TENSIONE 230V PER ALIMENTAZIONE E CONTROLLO DEGLI APPARECCHI DI EMERGENZA LED ALIMENTAZIONE 230V - TENSIONE IN USCITA 230V - IL LINE DI USCITA PER ALIMENTAZIONE E CONTROLLO DELLE LAMPADINE DI EMERGENZA 4 INGRESSI PROGRAMMABILI A TENSIONE DI RETE A 230 VAC UTILIZZABILI PER ATTIVAZIONE DI EMERGENZA LOCALE INGRESSI DIGITALI UTILIZZABILI COME SONAL E MODO PROGRAMMABILE CARGO MASSIMO PER CIRCUITO 80W - 20 LAMPADINE AUTONOMA 1h - 480W MARCA "ENERGY" MODELLO "SPR CENTER 10" CODICE SC2004
	PIATONERA EMERGENZA 12W LED - 120lm ALIMENTATA DA SISTEMA CENTRALIZZATO, DA INCASSO O A PIATONE GRADO DI PROTEZIONE IP20, CLASSE II DI ISOLAMENTO MARCA "ENERGY" MODELLO "PRODOTTO" CODICE "P10000085-SC24"
	PIATONERA EMERGENZA 23W LED - 210lm ALIMENTATA DA SISTEMA CENTRALIZZATO, DA INCASSO O A PIATONE GRADO DI PROTEZIONE IP20, CLASSE II DI ISOLAMENTO MARCA "ENERGY" MODELLO "PRODOTTO" CODICE "P11000085-SC24"
	PIATONERA EMERGENZA 44W LED - 200lm ALIMENTATA DA SISTEMA CENTRALIZZATO, DA INCASSO O A PIATONE GRADO DI PROTEZIONE IP20, CLASSE II DI ISOLAMENTO MARCA "ENERGY" MODELLO "PRODOTTO" CODICE "P12000085-SC24"
	PIATONERA EMERGENZA 31W LED - 200lm ALIMENTATA DA SISTEMA CENTRALIZZATO, DA INCASSO O A PIATONE GRADO DI PROTEZIONE IP20, CLASSE II DI ISOLAMENTO MARCA "ENERGY" MODELLO "CRISTAL WALL" CODICE "C10000085-SC24"

TABELLE RIEPILOGATIVE CENTRALE SOCC1*


CARICO MASSIMO PER CIRCUITO: 80W - 20 LAMPADINE AUTONOMA: 1h - 480W (8 LINEE DI USCITA)

CENTRALE 1 Autonomia: 1h 24V	EM1	EM2	EM3	EM4	EM5	EM6	EM7	EM8
E1 1,2W	12	10	6		9	7	12	3
E2 2,3W		7	11					
E3 6,4W						7		6
EXT1 3,1W	4		5			1		2
TOT. Corpi Illuminanti	16	17	17	5	9	15	12	11
TOT. Assorbimento (W)	26,8W	28,1W	32,5W	15,5W	10,8W	56,3W	14,4W	48,2W
Lunghezza linea indicativa	140	150	130	130	100	120	130	150
Sezione cavo FTG180M16	2x2,5mmq	2x2,5mmq	2x2,5mmq	2x2,5mmq	2x4mmq	2x2,5mmq	2x4mmq	
POTENZA TOTALE - 232,6W								

TABELLE RIEPILOGATIVE CENTRALE SOCC2*

CARICO MASSIMO PER CIRCUITO: 80W - 20 LAMPADINE AUTONOMA: 1h - 480W (8 LINEE DI USCITA)

CENTRALE 2 Autonomia: 1h 24V	EM1	EM2	EM3	EM4	EM5	EM6
E1 1,2W	11	11				
E2 2,3W			16			
E3 6,4W	6					
EXT1 3,1W				6		
TOT. Corpi Illuminanti	17	11	16	6		
TOT. Assorbimento (W)	51,6W	13,2W	36,8W	18,6W		
Lunghezza linea indicativa	150	150	170	110		
Sezione cavo FTG180M16	2x4mmq	2x2,5mmq	2x4mmq	2x2,5mmq		
POTENZA TOTALE - 120,2W						

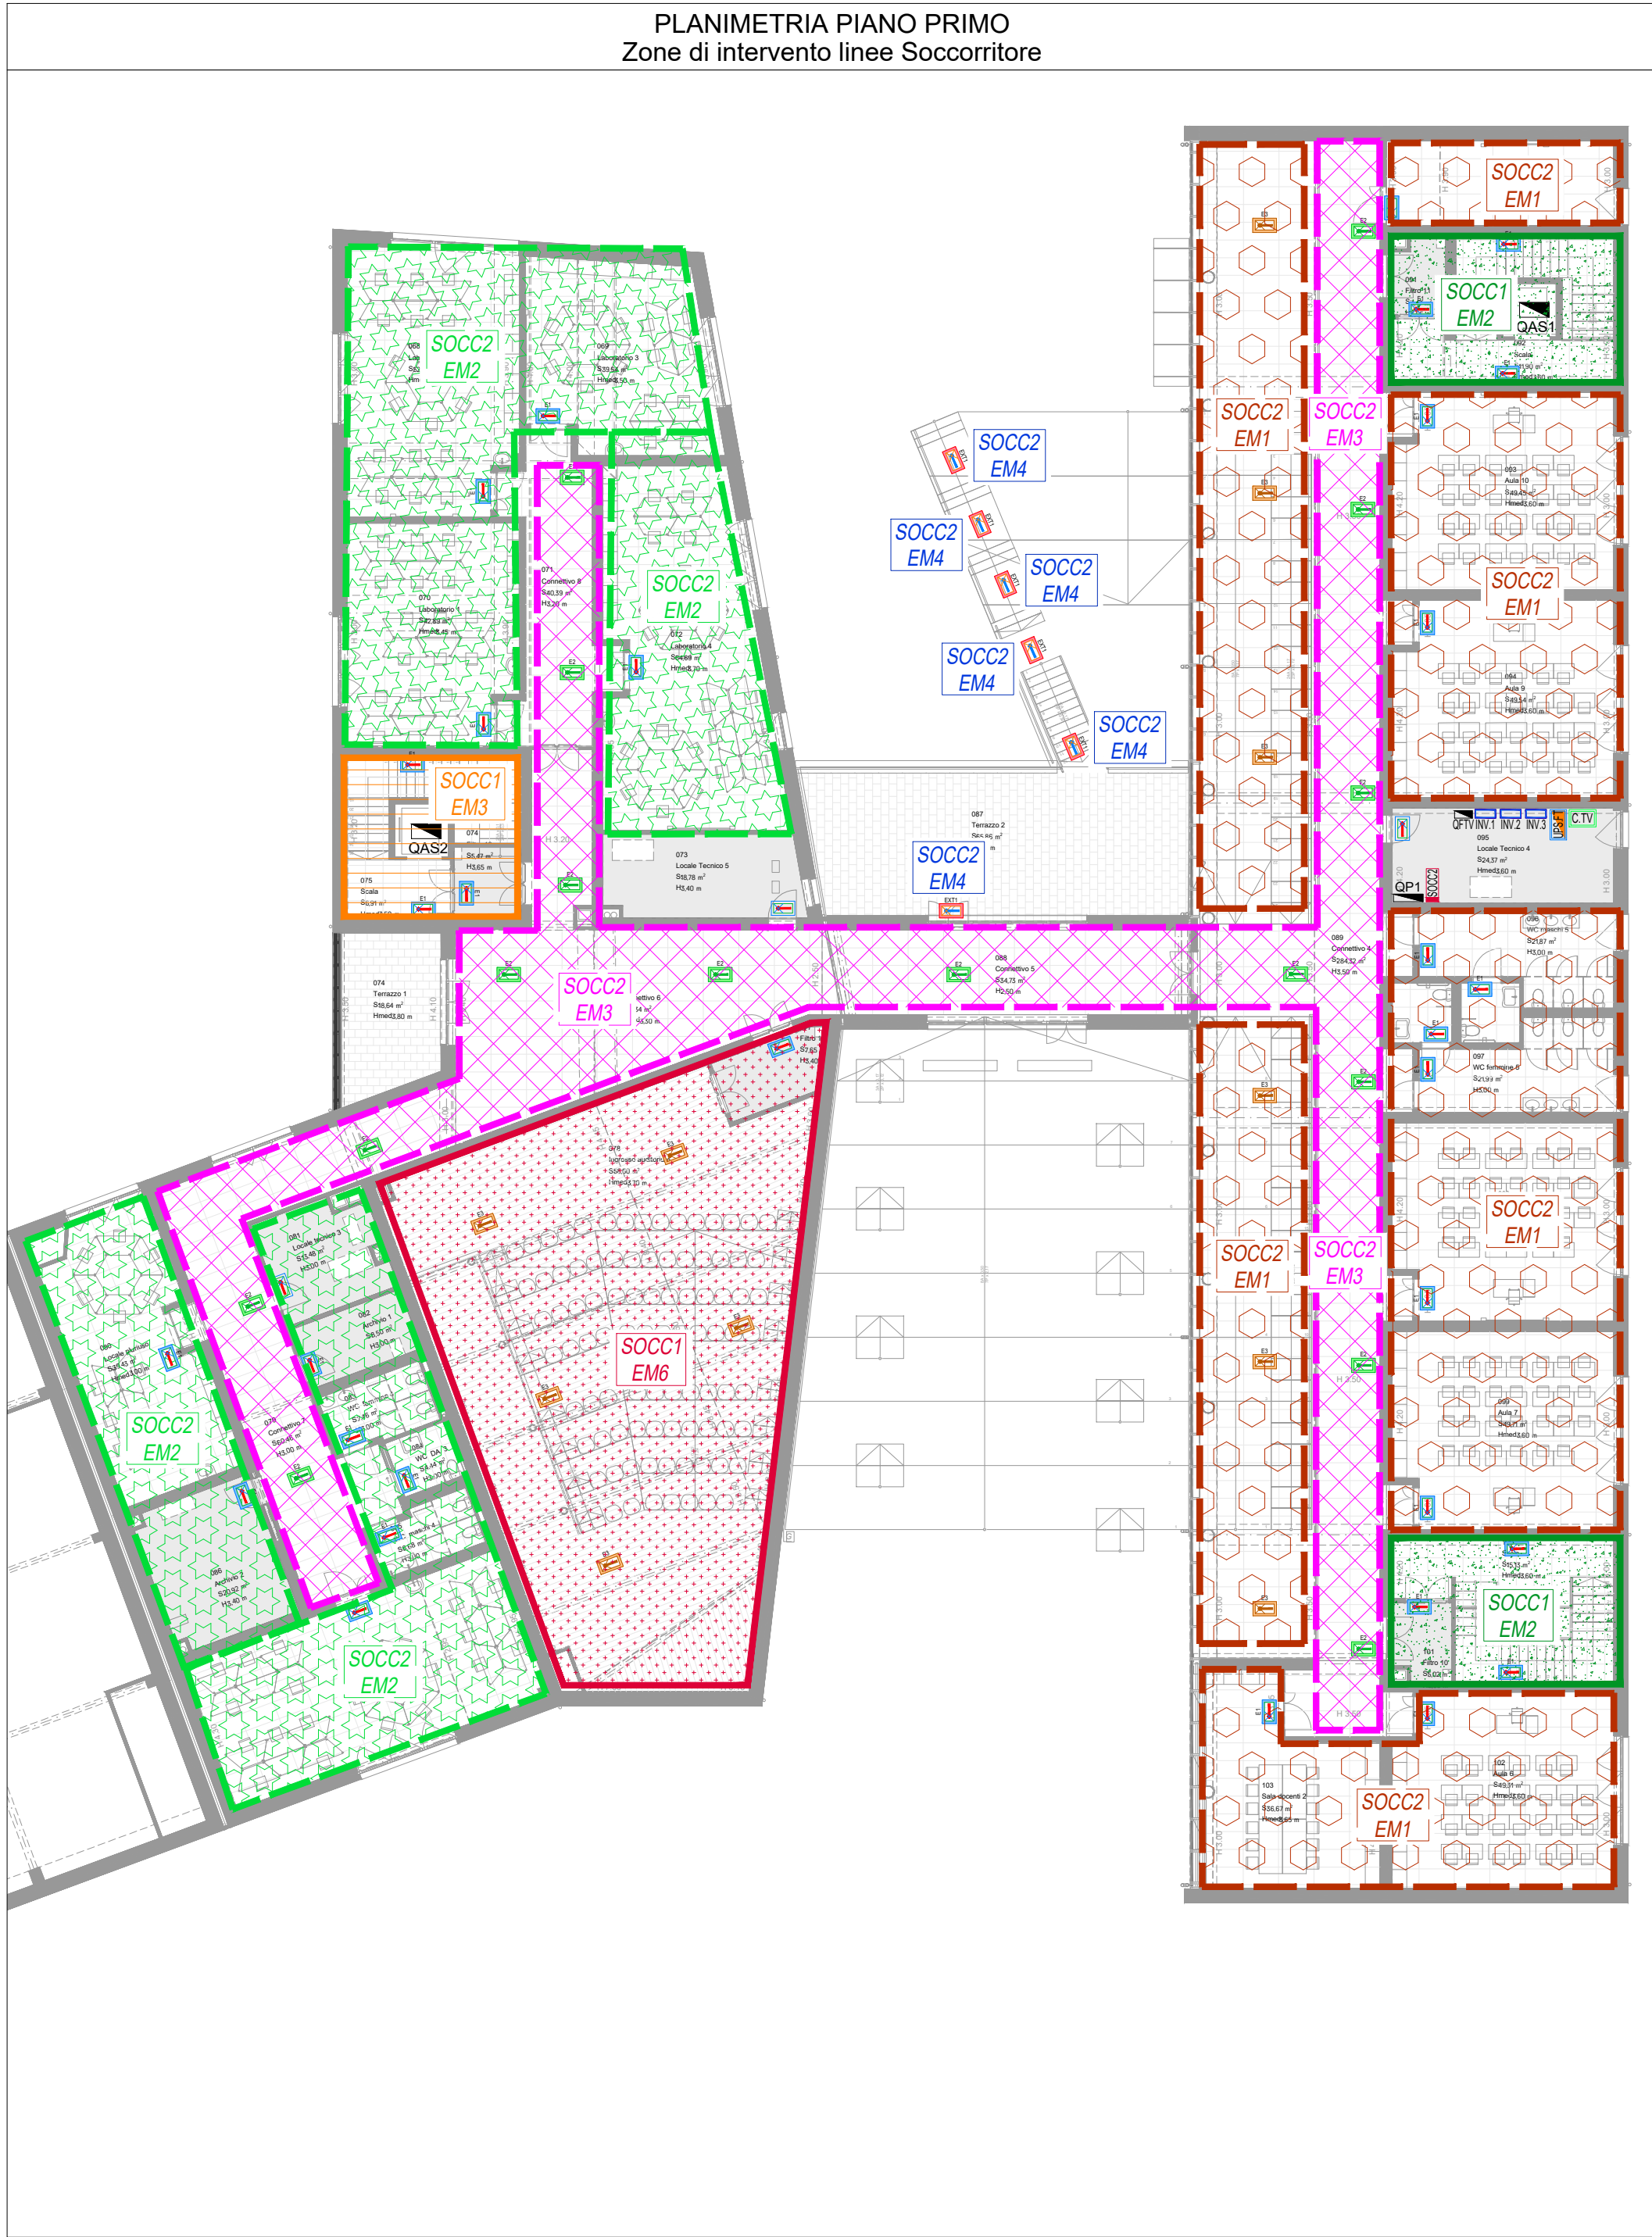

COMUNE DI POGGIBONSI
PROVINCIA DI SIENA

NUOVA SCUOLA "P. CALAMANDREI"
IN VIA ALDO MORO

PROGETTO ESECUTIVO

ATI DI PROGETTAZIONE:
MANDATARIA
EUTECNE
architettura | ingegneria

MANDANTI
SINERGIE
Via G. D'Adda, 18
20117 (Milano)
T +39 02 55555555
F +39 02 54444444
info@sinergie.it
www.sinergie.it

COMMITTENTE
COMUNE DI POGGIBONSI
R.U.P. Arch. Vito Desabato

GRUPPO DI PROGETTAZIONE
Dott. Arch. Pierpaolo PAPI
Dott. Ing. Luca DELL'AMENDANO
Dott. Ing. Martina RICCIO
Ing. Silvia ANTONELLI

Dott. Arch. Olimpia LORENZINI
Dott. Arch. Luca FRAPPI
Dott. Arch. Debora PALLUMMO

Dott. Geol. Armando GRAZI
Dott. Ing. Paolo BIANCHI
Dott. Ing. Carlo BIANCHI

TITOLO
IMPIANTI ELETTRICI
Impianto illuminazione di sicurezza

COMMESSA
C34E

ELABORATO
ED3

REVISIONE
B

SCALA
1:200

REV. N.	DATA	MOTIVO DELLA EMISSIONE	ESEGUITO	CONTROLLATO	APPROVATO
A	APR 2021	PROGETTO ESECUTIVO		F. ARDINO	F. FRAPPI
B	GEN 2024	PROGETTO ESECUTIVO - VERIFICA		P. PAPI	F. FRAPPI