

COMUNE DI POGGIBONSI

PROVINCIA DI SIENA

NUOVA SCUOLA "P. CALAMANDREI"
IN VIA ALDO MORO

PROGETTO ESECUTIVO

ATI DI PROGETTAZIONE:

MANDATARIA

EUTECNE S.r.l.
architettura | ingegneria

Via Romana, 30
06126 Perugia
T +39 075 32 761
F +39 075 34 470

Via Roma, 20/a
57034 Campo nell'Elba (LI)
Isola d'Elba
T/F +39 0565 977 589

office@eutecne.it
www.eutecne.it

RESPONSABILE DELLA PROGETTAZIONE
ING. FEDERICO FRAPPI

MANDANTI



Via G. Di Vittorio, 15
20017 Rho (MI)
T +39 02 93900835
F +39 02 93904566

progetti@retesinergie.it
www.retesinergie.it

COMMITTENTE:



COMUNE DI POGGIBONSI

R.U.P. Arch. Vito Disabato

GRUPPO DI PROGETTAZIONE

Dott. Arch. Pierpaolo PAPI
Dott. Ing. Luca DELL'AVERSANO
Dott. Ing. Martina RICCI
Ing. Sonia ANTONELLI

Dott. Arch. Olimpia LORENZINI
Dott. Arch. Luca FRAPPI
Dott. Arch. Debora PALUMMO

Dott. Geol. Armando GRAZI
Dott. Ing. Paolo BINDI
Dott. Ing. Dario BANDI


TITOLO **LAYOUT DI CANTIERE**

COMMESSA	ELABORATO	REVISIONE
C34E	ZL1	B

SCALA --


REV. N	DATA	MOTIVO DELLA EMISSIONE	ESEGUITO	CONTROLLATO	APPROVATO
A	APR.2021	PROGETTO ESECUTIVO	LDA	F.ARDINO	F.FRAPPI
B	GEN.2024	PROGETTO ESECUTIVO - VERIFICA	E.SCIATTELLA	P.PAPI	F.FRAPPI

ALLESTIMENTO AREA DI CANTIERE

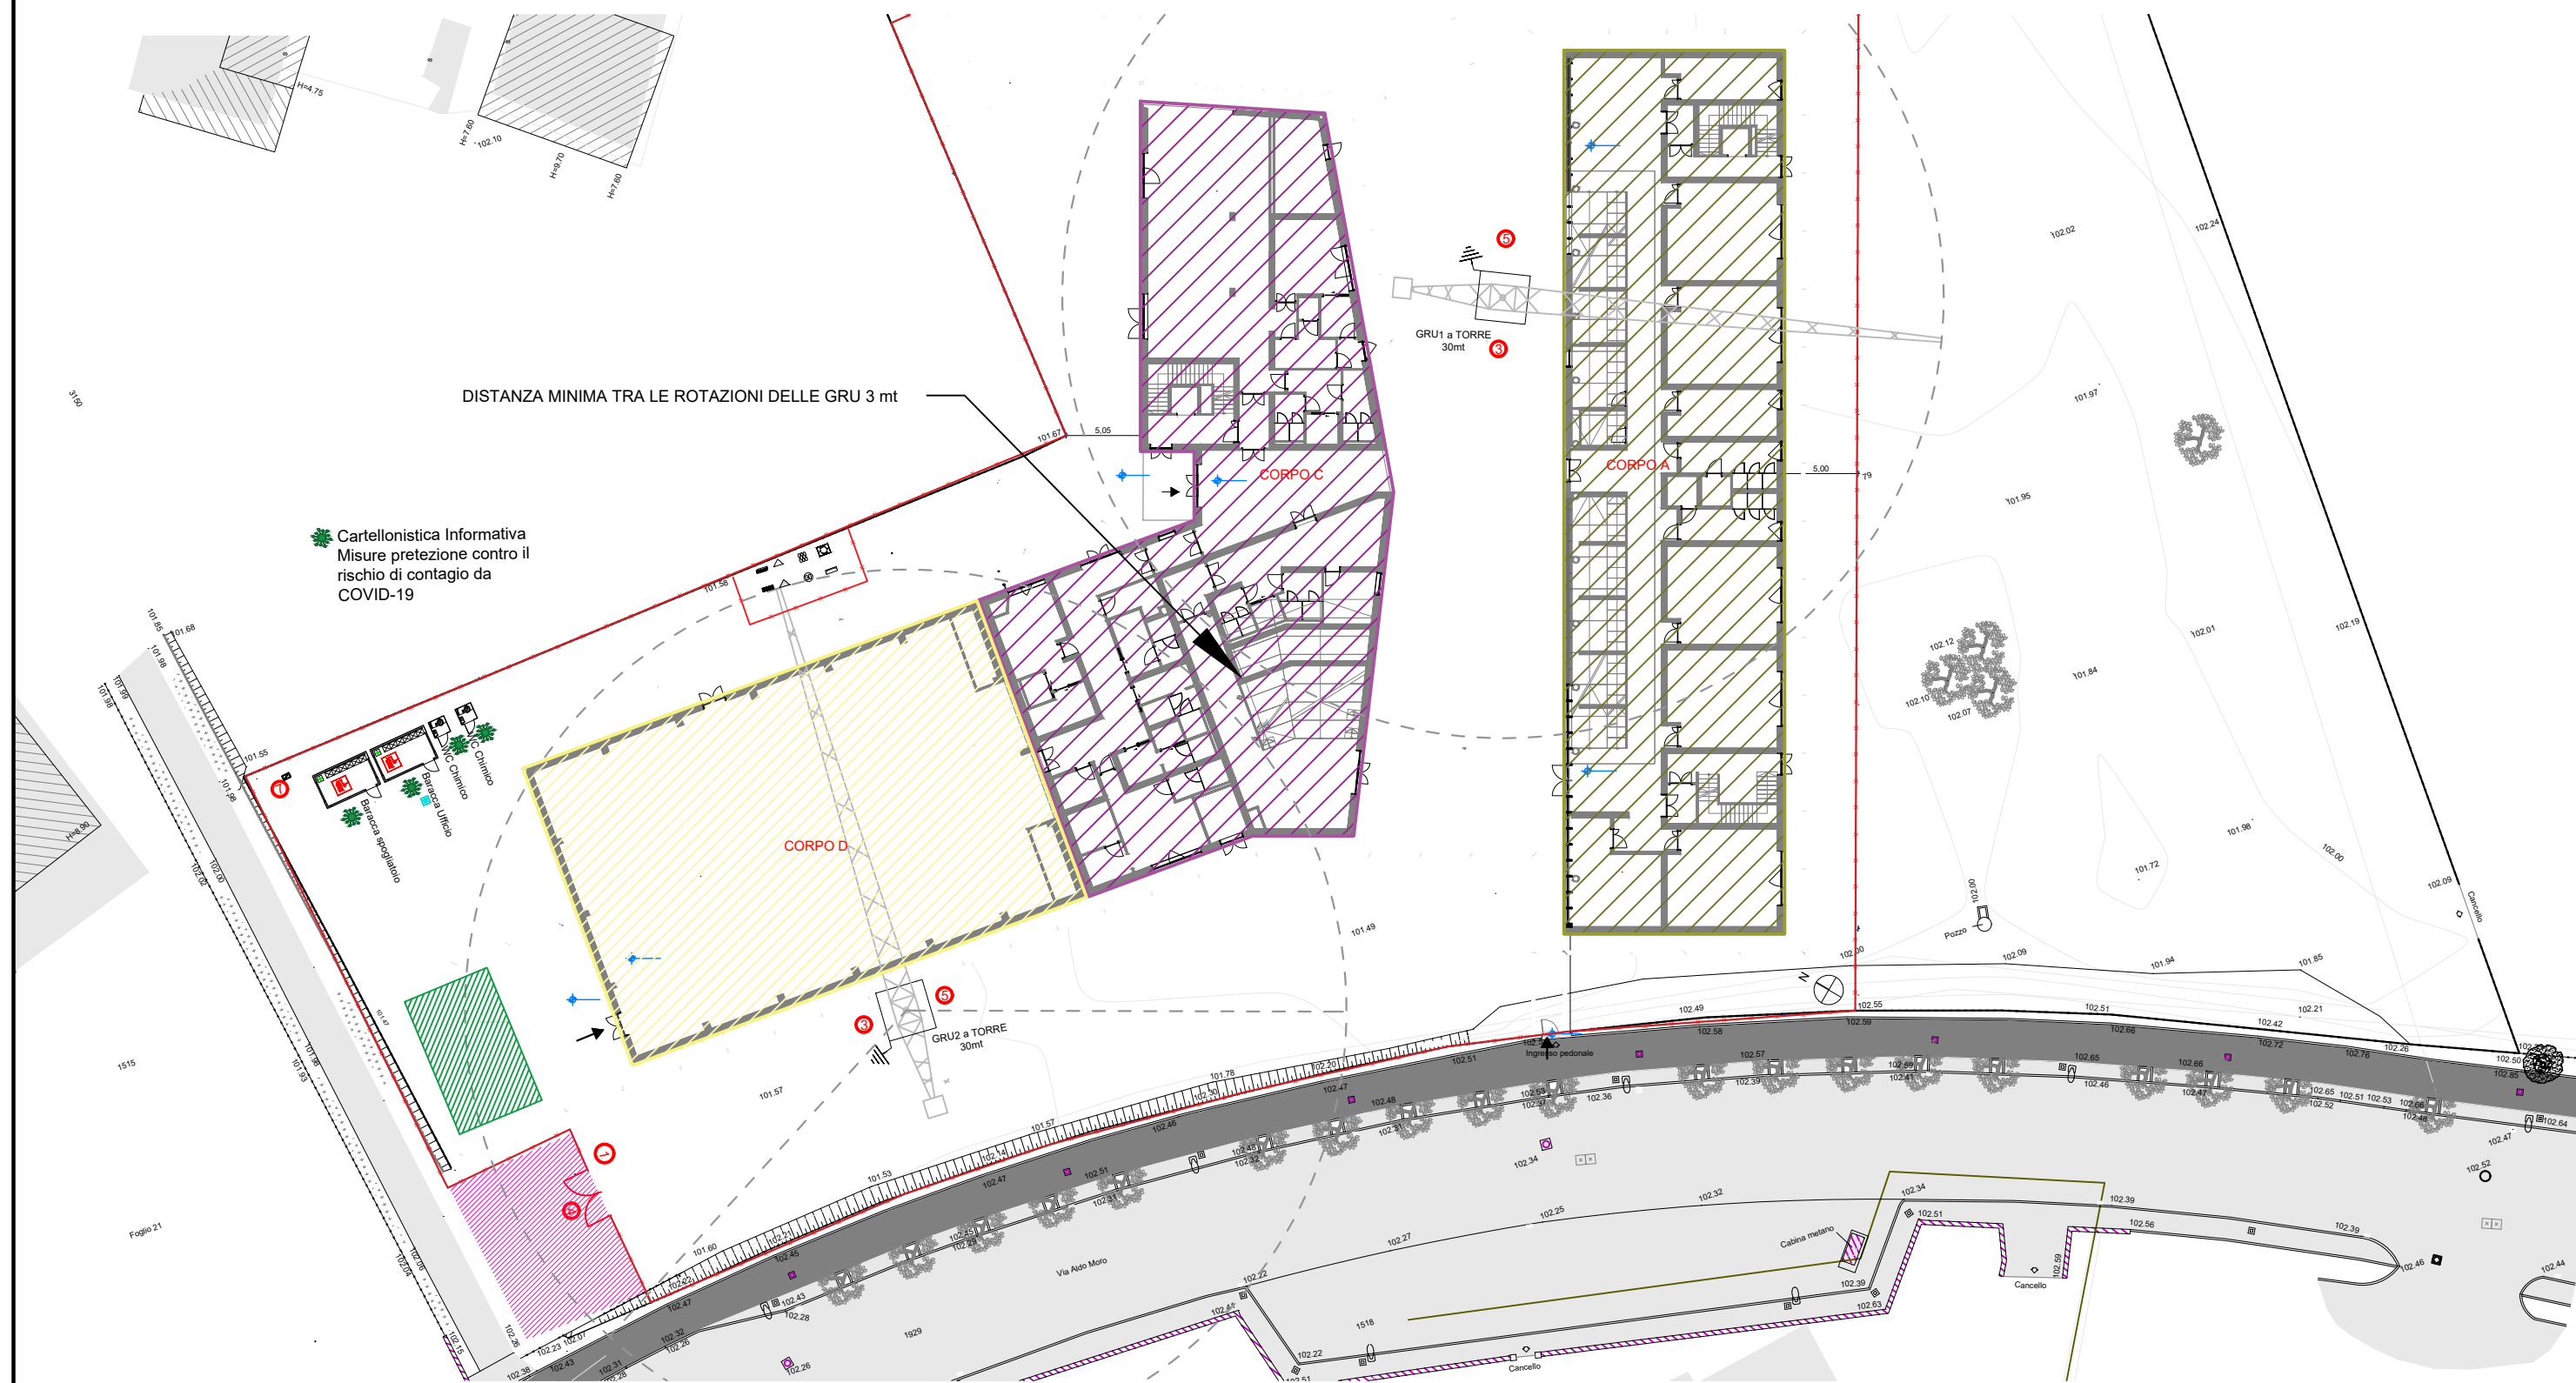

SISTEMAZIONE PONTEGGI PIANTA


scala 1:250

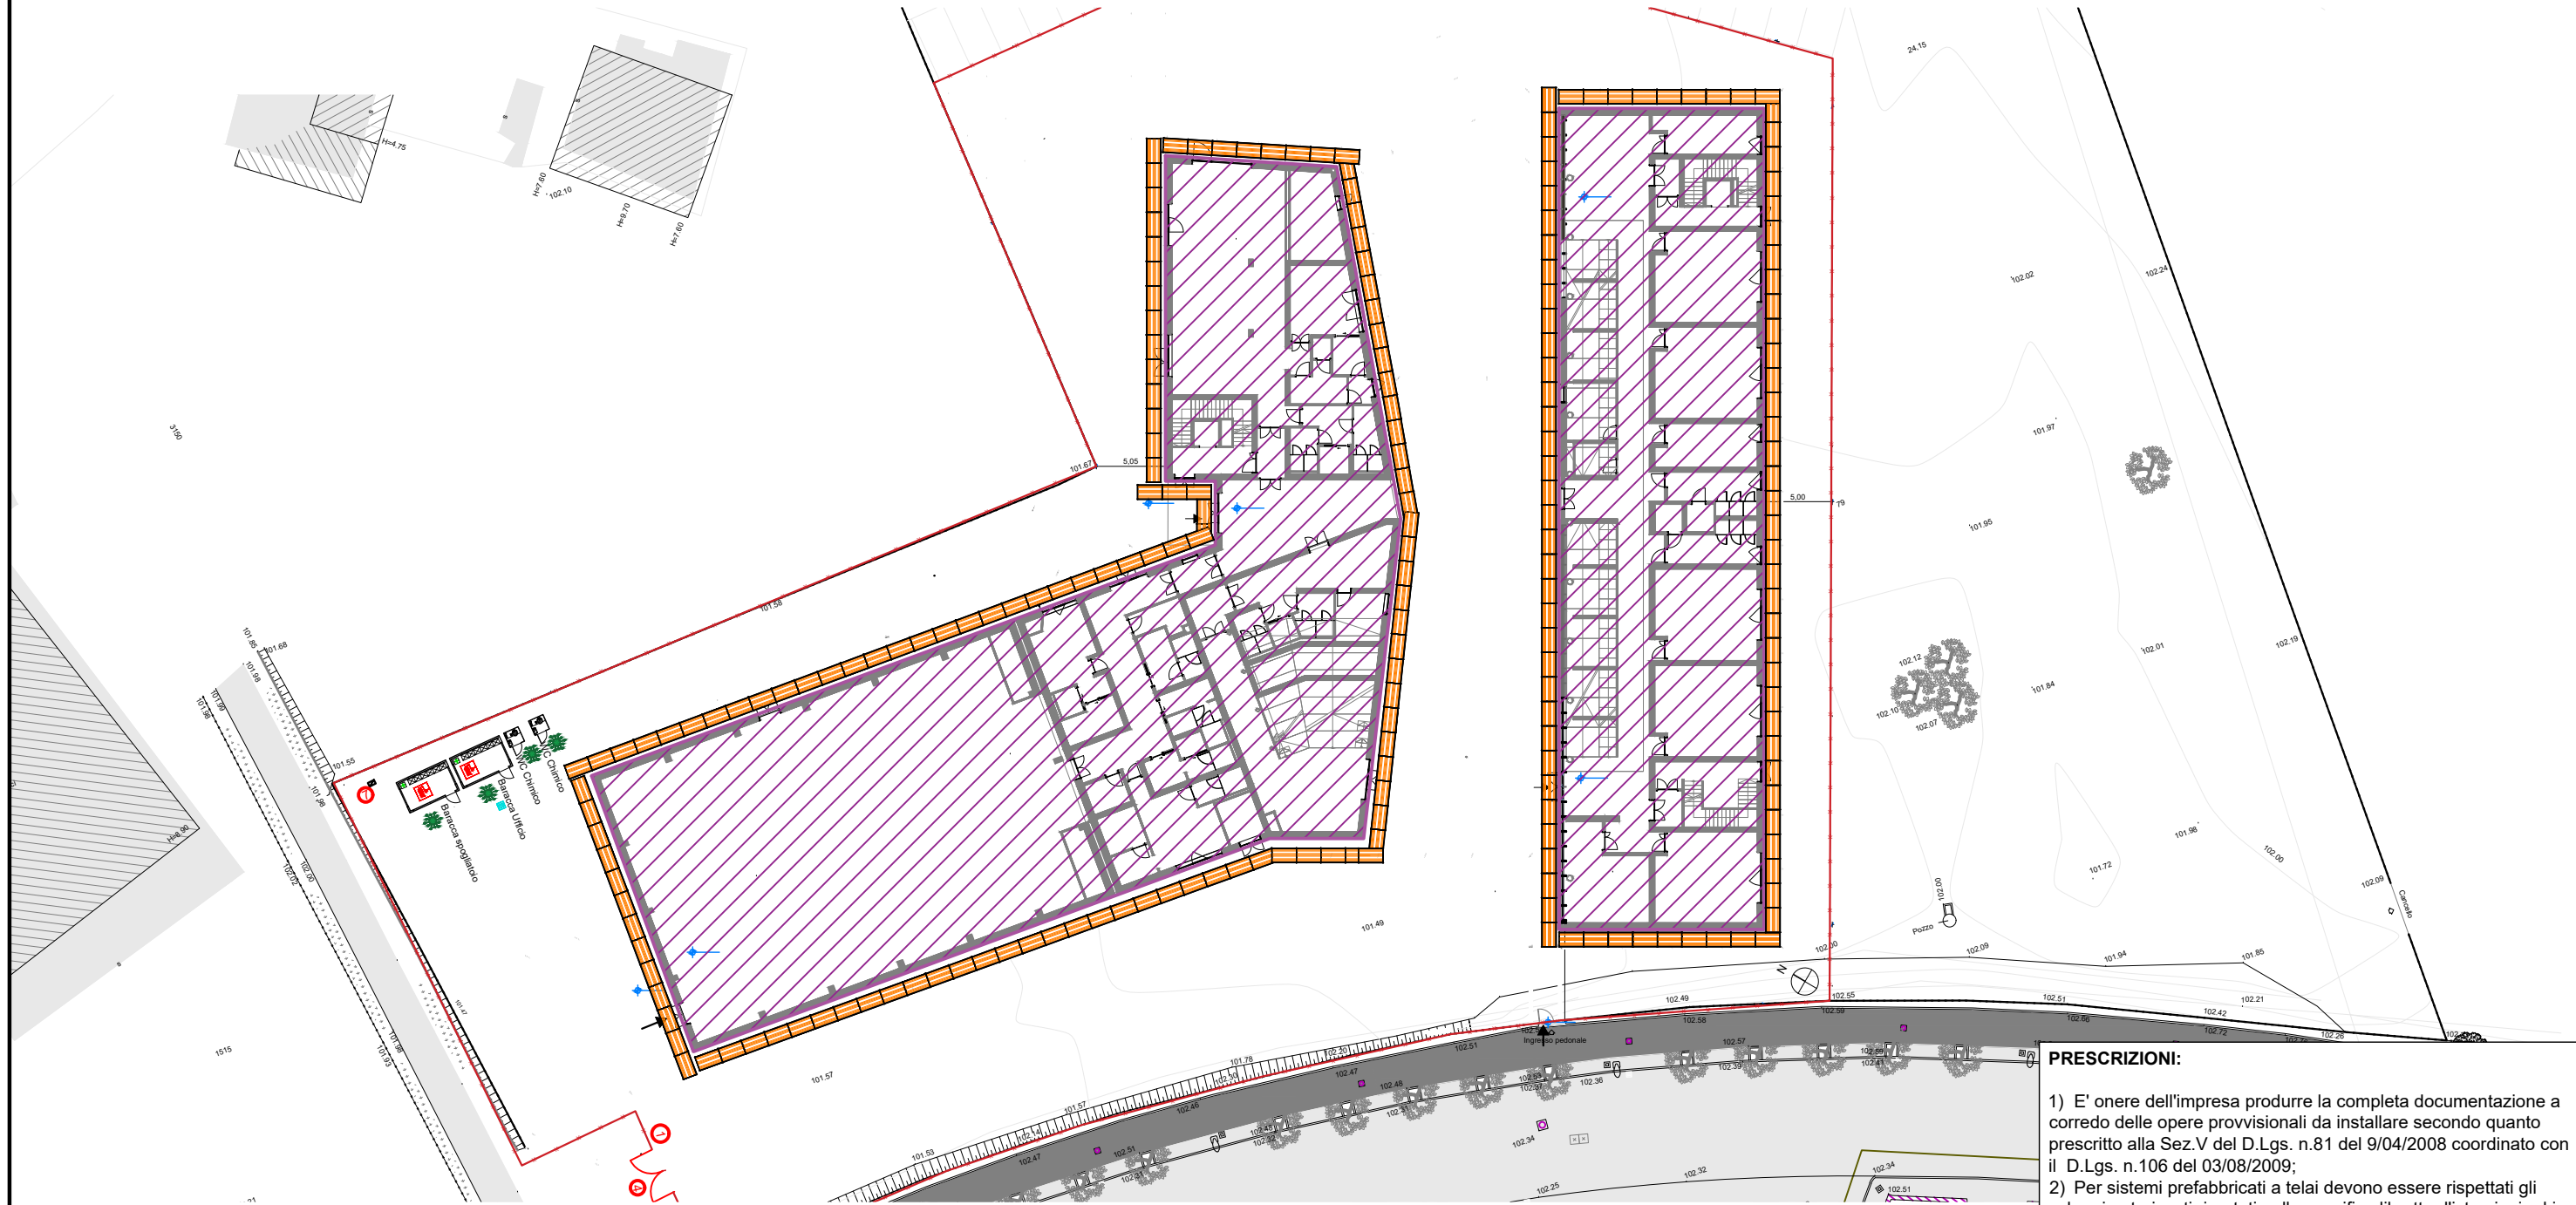

⑥ PONTEGGI
Segnaletica di sicurezza



MODULI BASE

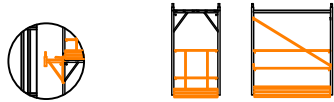

N.B.
Dove necessario si deve procedere alla posa in opera di mensole interne tale da peremtttere la realizzazione di un piano di calpestio privo di fessure posto alla distanza massima di 20cm dalla linea di ingombro del fabbricato (art. 138 comma 2 D.Lgs 81/08)

PRESCRIZIONI:

- 1) E' onere dell'impresa produrre la completa documentazione a corredo delle opere provvisoria da installare secondo quanto prescritto alla Sez.V del D.Lgs. n.81 del 9/04/2008 coordinato con il D.Lgs. n.106 del 03/08/2009;
- 2) Per sistemi prefabbricati a telai devono essere rispettati gli schemi autorizzati riportati nello specifico libretto d'istruzioni ed i relativi limiti di impiego;
- 3) Gli ancoraggi devono essere in misura di almeno uno ogni 20mq e realizzati in conformità delle prescrizioni riportate nello specifico libretto d'istruzioni;
- 4) I nodi devono essere bloccati mediante l'attivazione dei relativi dispositivi di sicurezza;
- 5) E' consentito un distacco massimo del piano di calpestio della parete non superiore a 20cm (art. 138 comma 2 D.Lgs 81/08); qualora sia necessario coprire distanze maggiori sarà onere dell'impresa ricorrere all'uso di mensole tali da garantire il rispetto del requisito minimo richiesto.
- 6) Il sovraccarico complessivo in proiezione verticale non deve superare quello adottato per la verifica di stabilità del ponteggio;
- 7) La superficie esposta all'azione del vento, per ciascun modulo, non può esse superiore a quella presa in considerazione nella apposita verifica di stabilità;
- 8) Qualora si apportino modifiche alle condizioni d'uso dei ponteggi a telai prefabbricati è onere dell'impresa produrre la necessaria documentazione di calcolo in conformità alle norme vigenti;
- 9) E' onere dell'impresa l'integrazione del ponteggio con elementi giunto tubo;
- 10) E' pnere dell'impresa il progetto del ponteggio.