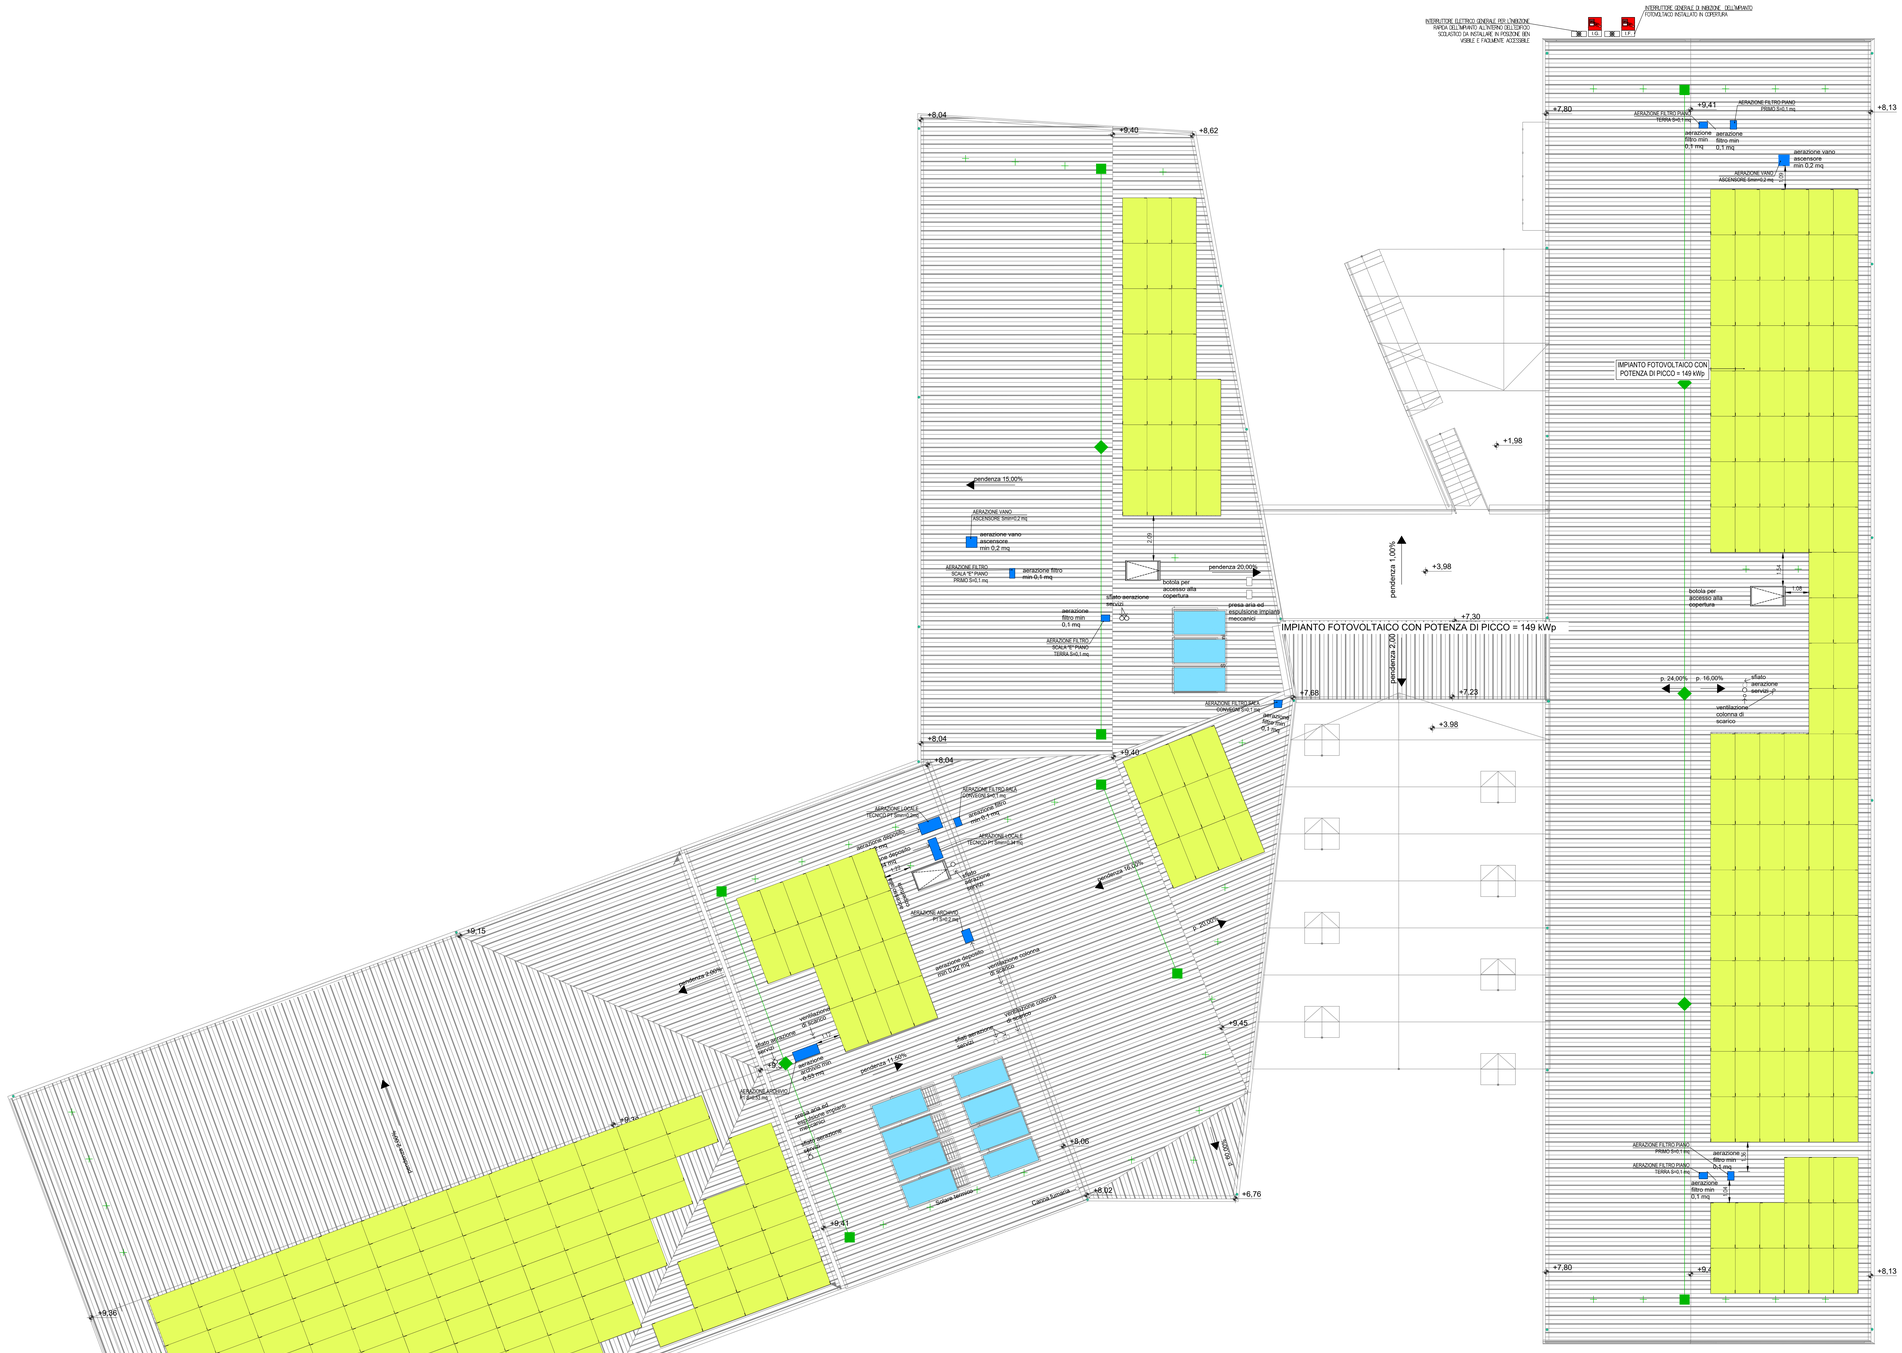

PIANTA COPERTURA - scala 1:100

LEGENDA PREVENZIONE INCENDI

- PORTA EI 120
- PORTA EI 60
- PORTA EI 30
- FRONTIERA REI 120
- FRONTIERA REI 60
- FRONTIERA REI 30
- CARTELLI SEGNALATORI
- LAMPADA DI EMERGENZA CON PITTOGRAMMA
- INDICAZIONI VIE DI ESODO
- VIA D'USCITA VERSO L'ALTO
- VIA D'USCITA ORIZZONTALE
- VIA D'USCITA VERSO IL BASSO
- MANIGLIA ANTIPANICO
- LUCE DI EMERGENZA
- INTERRUTTORE GENERALE
- ELETTROMAGNETI PER PORTE TAGLIAFUOCO
- CARTELLO SEGNALATORE DI ESTINTORE AD ANIDRIDE CARBONICA
- SUPERFICIE DI AREAZIONE
- BOCCA D'INCENDIO UNI 45 INCASSATA A PARETE-MANICHETTA DA 20 mt
- BOCCA D'INCENDIO UNI 45 ESTERNA CON CASSETTA-MANICHETTA DA 20 mt
- ATTACCO PER AUTOPOMPA VV.F. UNI 70
- NASPO ANTINCENDIO SU SUPPORTO ORIENTABILE A MURO DN 25
- IDRANTE SOPRASUOLO UNI 65 UNI 70 X 2
- RIVELATORE DI FUMO
- RIVELATORE DI GAS
- RILEVATORE OTTICO DI FUMO LINEARE CON CATARIFRANGENTE
- ALLARME ACUSTICO
- PULSANTE DI ALLARME
- ESTINTORE PORTATILE DA 6 Kg

COMUNE DI POGGIBONSI
PROVINCIA DI SIENA

NUOVA SCUOLA "P. CALAMANDREI"
IN VIA ALDO MORO

PROGETTO ESECUTIVO

ATI DI PROGETTAZIONE:

MANDATARIA

EUTECNE s.r.l.
architettura | ingegneria

Via Pomeria, 20
06135 Perugia
T +39 075 32 781
F +39 075 34 470

Via Roma, 20/A
57034 Campo nell'Elba (LI)
Isola d'Elba
T/F +39 0565 977 589

office@eutecne.it
www.eutecne.it

MANDANTI

SINERGIE s.r.l.

Via G. Di Vittorio, 15
20017 Rho (MI)
T +39 02 93900835
F +39 02 93904566

progetti@retesinergie.it
www.retesinergie.it

RESPONSABILE DELLA PROGETTAZIONE
ING. FEDERICO FRAPPI

GRUPPO DI PROGETTAZIONE

Dott. Arch. Pierpaolo PAPI
Dott. Ing. Luca DELL'AVERSANO
Dott. Ing. Martina RICCI
Ing. Sonia ANTONELLI
Dott. Arch. Olimpia LORENZINI
Dott. Arch. Luca FRAPPI
Dott. Arch. Debora PALUMMO
Dott. Geol. Armando GRAZI
Dott. Ing. Paolo BINDI
Dott. Ing. Dario BANDI

COMMITTENTE:

COMUNE DI POGGIBONSI
R.U.P. Arch. Vito Disabato

TITOLO PIANTA COPERTURA PREVENZIONE INCENDI

COMMESSA	ELABORATO	REVISIONE
C34E	P4	B
SCALA	1:100	

REV. N	DATA	MOTIVO DELLA EMISSIONE	ESEGUITO	CONTROLLATO	APPROVATO
A	APR.2021	PROGETTO ESECUTIVO		F.ARDINO	F.FRAPPI
B	GEN.2024	PROGETTO ESECUTIVO - VERIFICA		P.PAPI	F.FRAPPI