
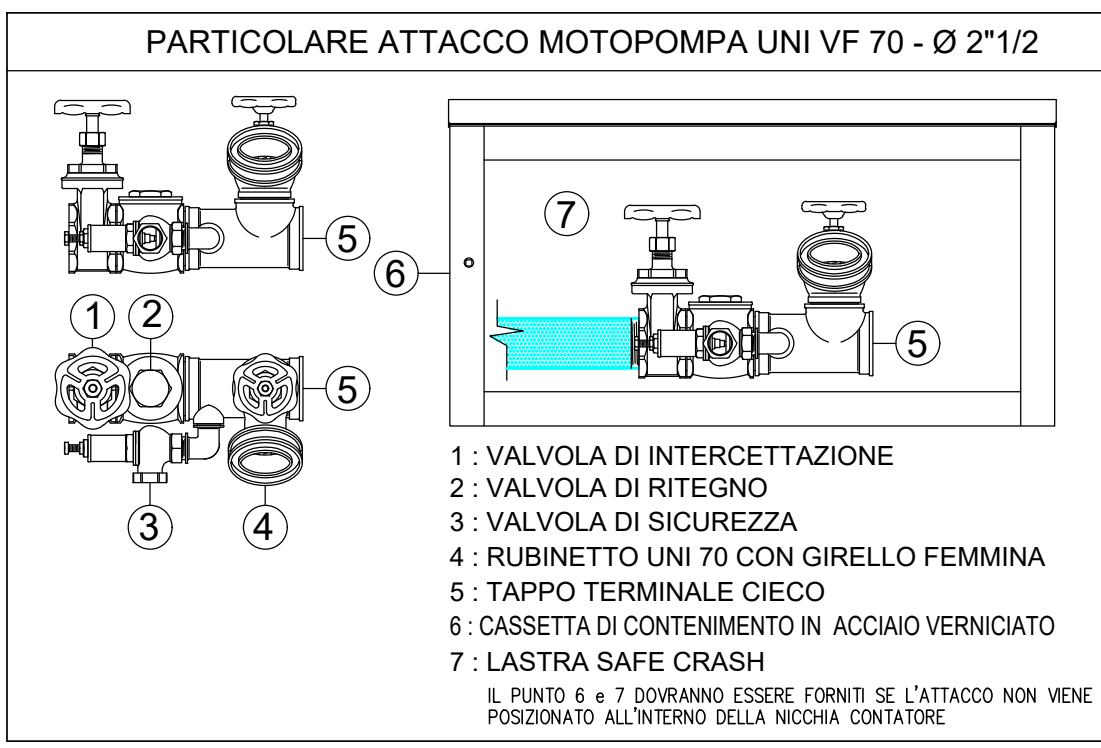


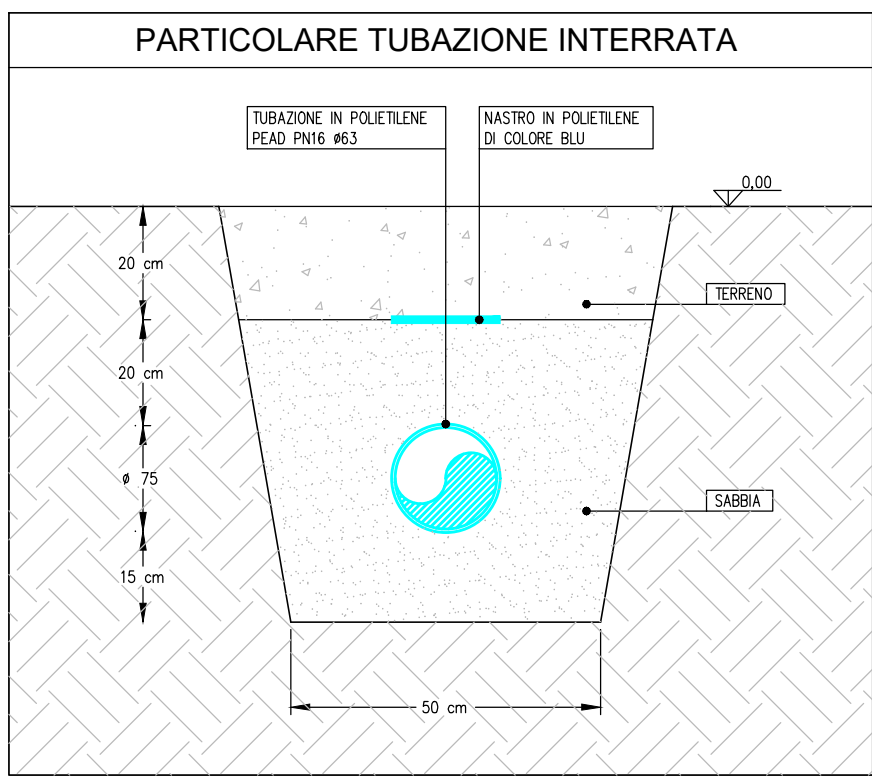

LEGENDA TUBAZIONI	
A) IMPIANTO IDRICO-ANTINCENDIO	---
* TUBAZIONI IN POLIETILENE AD ALTA DENSITA' PEAD PN16 A NORMA UNI 10910 CON GIUNZIONI MEDIANTE SALDATURA DI TESTA (TRATTI ESTERNI INTERRATI)	---
* TUBAZIONI IN ACCIAIO ZINCATO TIPO FM SERIE LEGGERA UNI 8863 CON GIUNZIONI MEDIANTE RACCORDI FILETTATI ISOLATE CON GUAINA IN ELASTOMERO ESTRUSO A CELLE CHIUSE E FINTURA ESTERNA, NEI TRATTI IN VISTA IN LAMIERINO DI ALLUMINIO (TRATTI INTERNI ED ESTERNI CORRENTI IN VISTA)	---


LEGENDA PREVENZIONE INCENDI	
PORTA EI 120	SUPERFICIE DI AREAZIONE
PORTA EI 60	BOCCA D'INCENDIO UNI 45 INCASSATA A PARETE-MANICHETTA DA 20 mt
PORTA EI 30	BOCCA D'INCENDIO UNI 45 ESTERNA CON CASSETTA-MANICHETTA DA 20 mt
FRONTIERA REI 120	ATTACCO PER AUTOPOMPA V.V.F. UNI 70
FRONTIERA REI 60	NASPO ANTINCENDIO SU SUPPORTO ORIENTABILE A MURO DN 25
FRONTIERA REI 30	IDRANTE SOPRASUOLO UNI 65 UNI 70 X 2
CARTELLI SEGNALETORI	RIVELATORE DI FUMO
LAMPADA DI EMERGENZA CON PITTOGRAMMA	RIVELATORE DI GAS
INDICAZIONI VIE DI ESODO	RIVELATORE OTTICO DI FUMO LINEARE CON CATARIFRANGENTE
VIA D'USCITA VERSO L'ALTO	ALLARME ACUSTICO
VIA D'USCITA ORIZZONTALE	PULSANTE DI ALLARME
VIA D'USCITA VERSO IL BASSO	ESTINTORE PORTATILE DA 6 Kg
MANIGLIA ANTIPANICO	
LUCE DI EMERGENZA	
INTERRUTTORE GENERALE	
ELETTROMAGNETI PER PORTE TAGLIAFUOCO	
CARTELLI SEGNALETORI DI ESTINTORE AD ANIDRIDE CARBONICA	

NOTA BENE

LA SEGNALEZIONE OTTICA E ACUSTICA, COSTITUITA DA:

- SIRENA ELETTRONICA PER INDICAZIONE POMPA IN MARCIA;
- LAMPEGGIANTE PER INDICAZIONE POMPA IN MARCIA (COLORE ROSSO);
- SIRENA ELETTRONICA PER L'INDICAZIONE DI MANCANZA FASE;
- LAMPEGGIANTE PER L'INDICAZIONE DI MANCANZA FASE (DI COLORE ARANCIONE);

DOVRÀ ESSERE RIPORTATA IN LUOGO DA CONCORDARE IN CANTIERE.

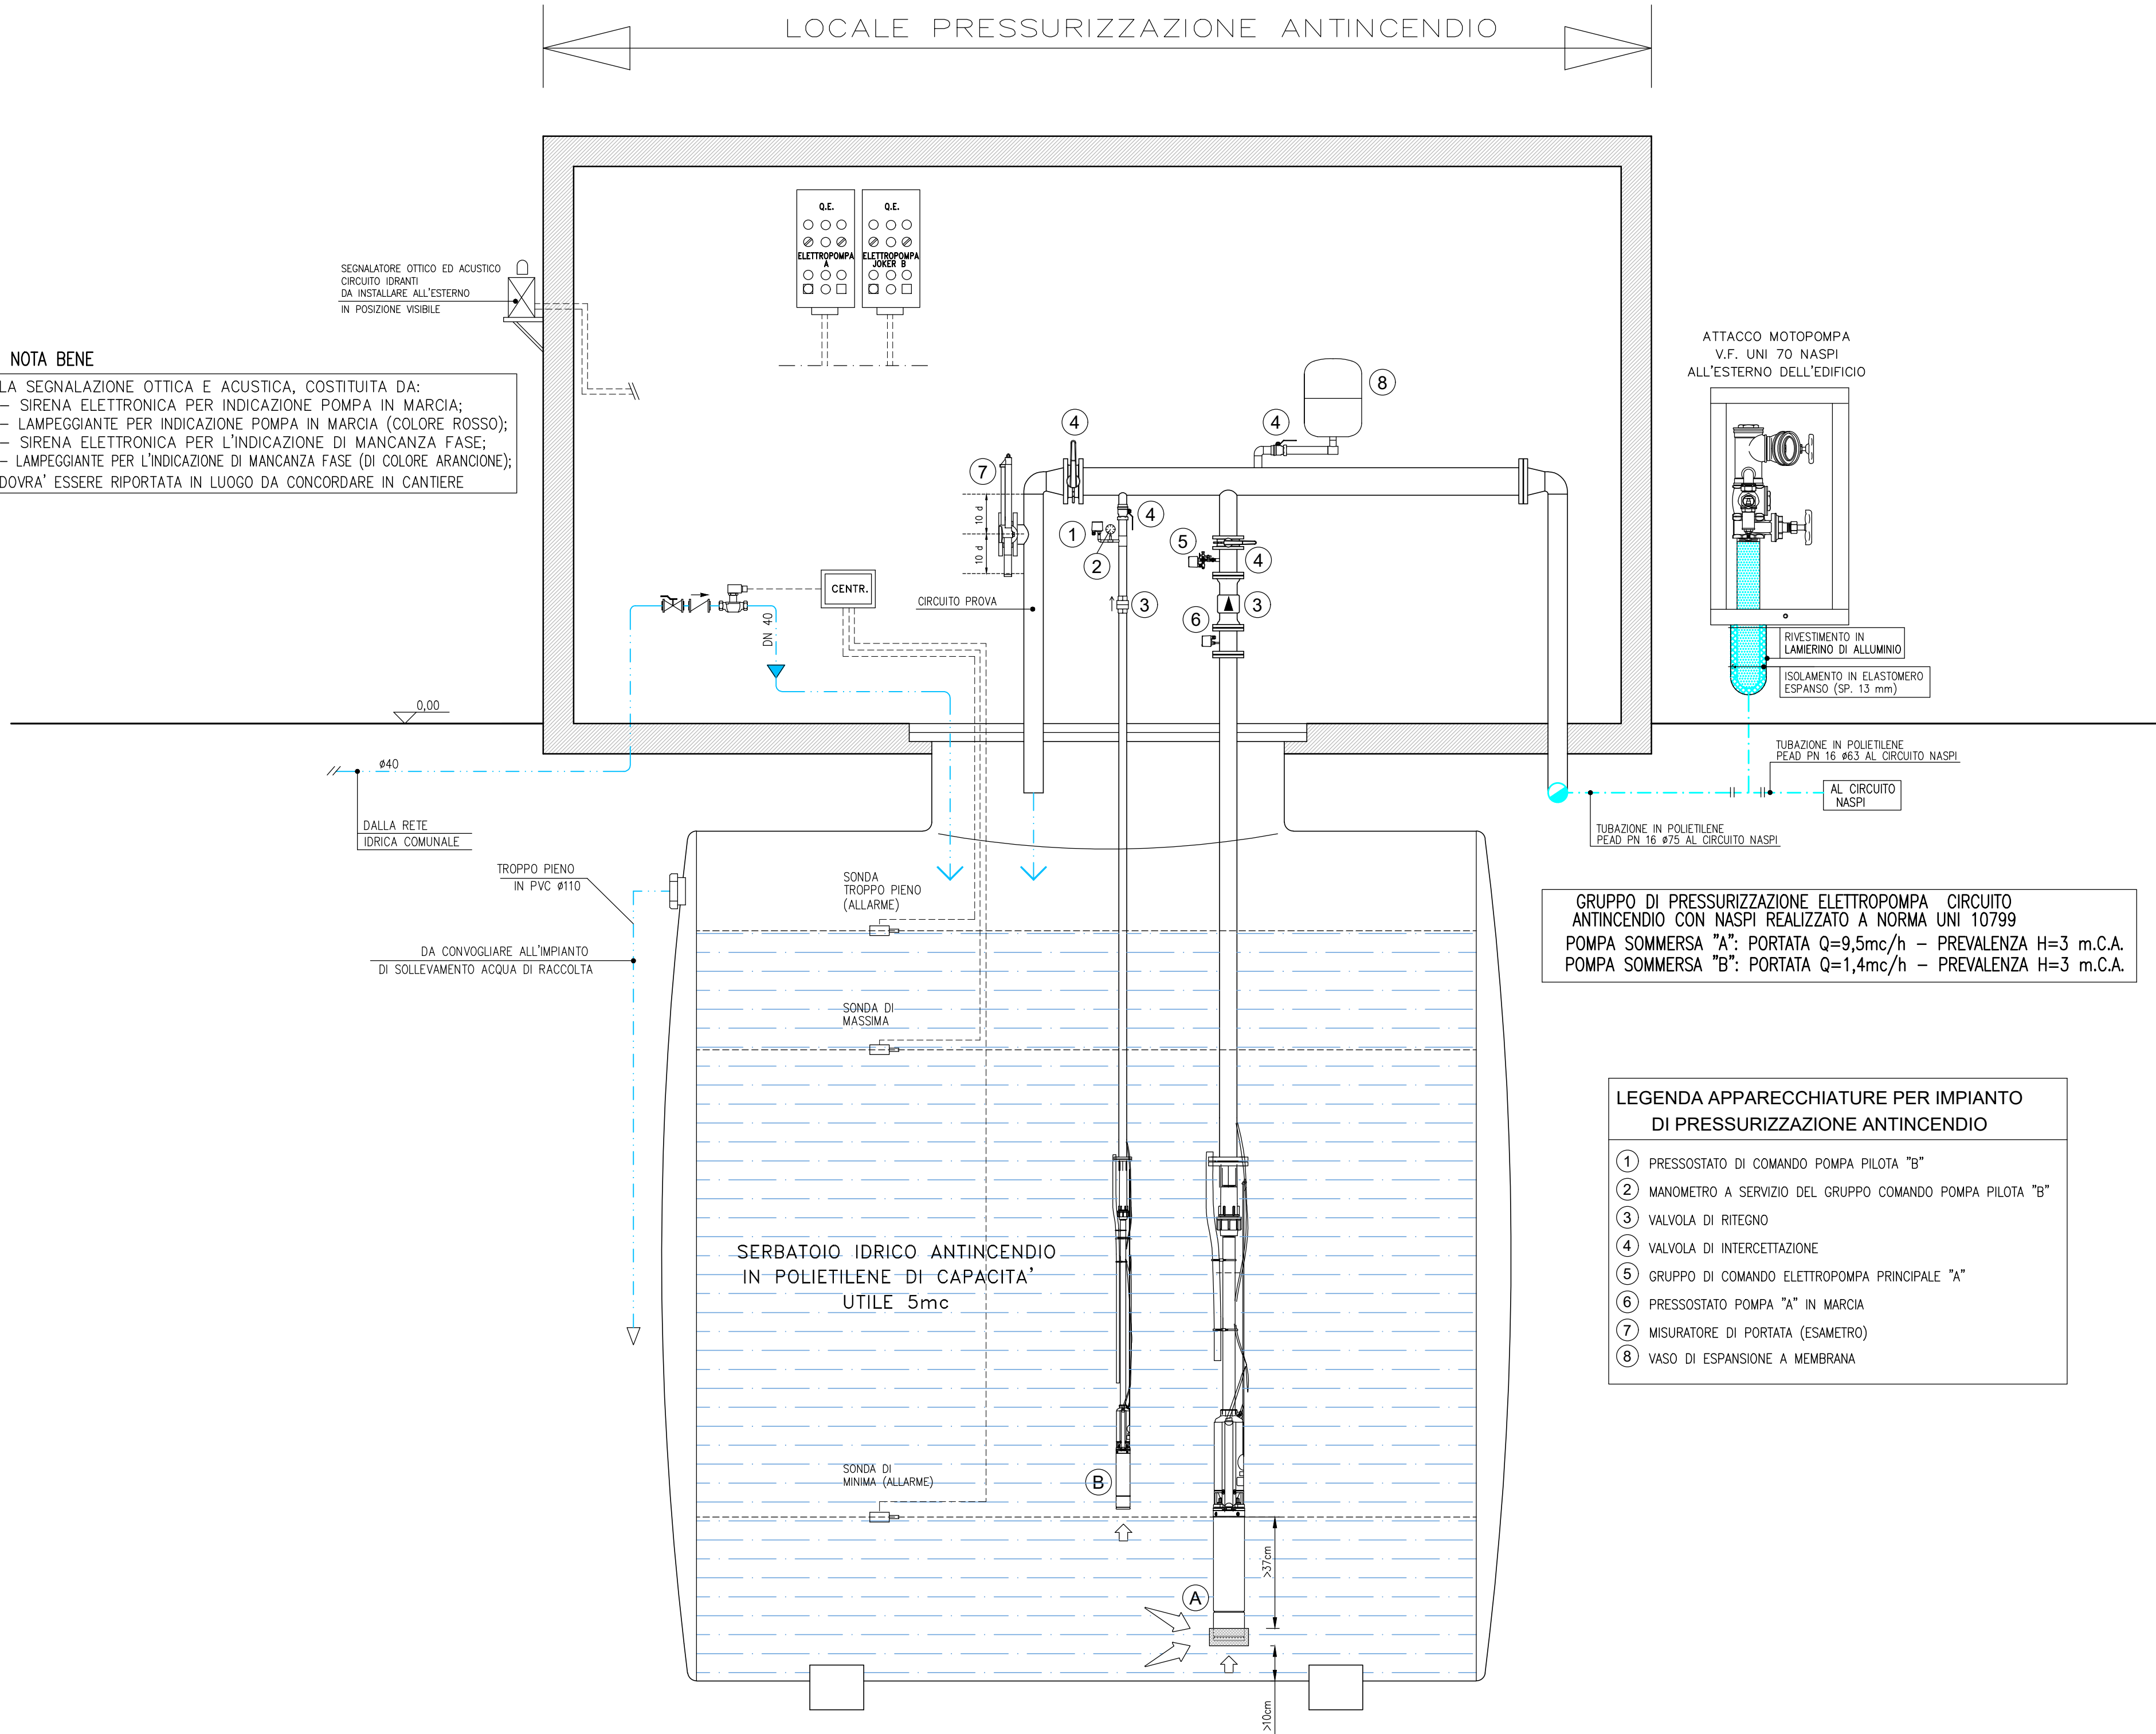

LEGENDA APPARECCHIATURE PER IMPIANTO DI PRESSURIZZAZIONE ANTINCENDIO	
1	PRESSOSTATO DI COMANDO POMPA PILOTA "B"
2	MANOMETRO A SERVIZIO DEL GRUPPO COMANDO POMPA PILOTA "B"
3	VALVOLA DI RITEGNO
4	VALVOLA DI intercettazione
5	GRUPPO DI COMANDO ELETTROPOMPA PRINCIPALE "A"
6	PRESSOSTATO POMPA "A" IN MARCIA
7	MISURATORE DI PORTATA (ESAMETRO)
8	VASO DI ESPANSIONE A MEMBRANA

COMUNE DI POGGIBONSI PROVINCIA DI SIENA

NUOVA SCUOLA "P. CALAMANDREI"
IN VIA ALDO MORO

PROGETTO ESECUTIVO

ATI DI PROGETTAZIONE:

MANDATARIA

EUTECNE
architettura | ingegneria

Via Roma, 30
00185 Perugia
T +39 075 52 701
F +39 075 34 470
Via Roma, 20/c
57034 Campo nell'Elba (LI)
Info: EBo
T/F +39 0565 977 589
office@eutecne.it
www.eutecne.it

RESPONSABILE DELLA PROGETTAZIONE
ING. FEDERICO FRAPPI

GRUPPO DI PROGETTAZIONE

Dott. Arch. Pierpaolo PAPI
Dott. Ing. Luca DELL'AVERSANO
Dott. Ing. Martina RICCI
Ing. Sonia ANTONELLI

MANDANTI

SINERGIE

Via G. Di Vittorio, 15
20017 Rho (MI)
T +39 02 50600835
F +39 02 50604566
progetti@retesnergie.it
www.retesnergie.it

COMMITTENTE:

COMMITTENTE:



COMUNE DI POGGIBONSI

R.U.P. Arch. Vito Disabato

TITOLO **SCHEMA FUNZIONALE LOCALE
PRESSURIZZAZIONE ANTINCENDIO**

COMMESSA ELABORATO REVISIONE

C34E P5 B

SCALA --- ---

REV. N	DATA	MOTIVO DELLA EMISSIONE	ESEGUITO	CONTROLLATO	APPROVATO
A	APR 2021	PROGETTO ESECUTIVO		F.ARDINO	F.FRAPPI
B	GEN 2024	PROGETTO ESECUTIVO - VERIFICA		P.PAPI	F.FRAPPI