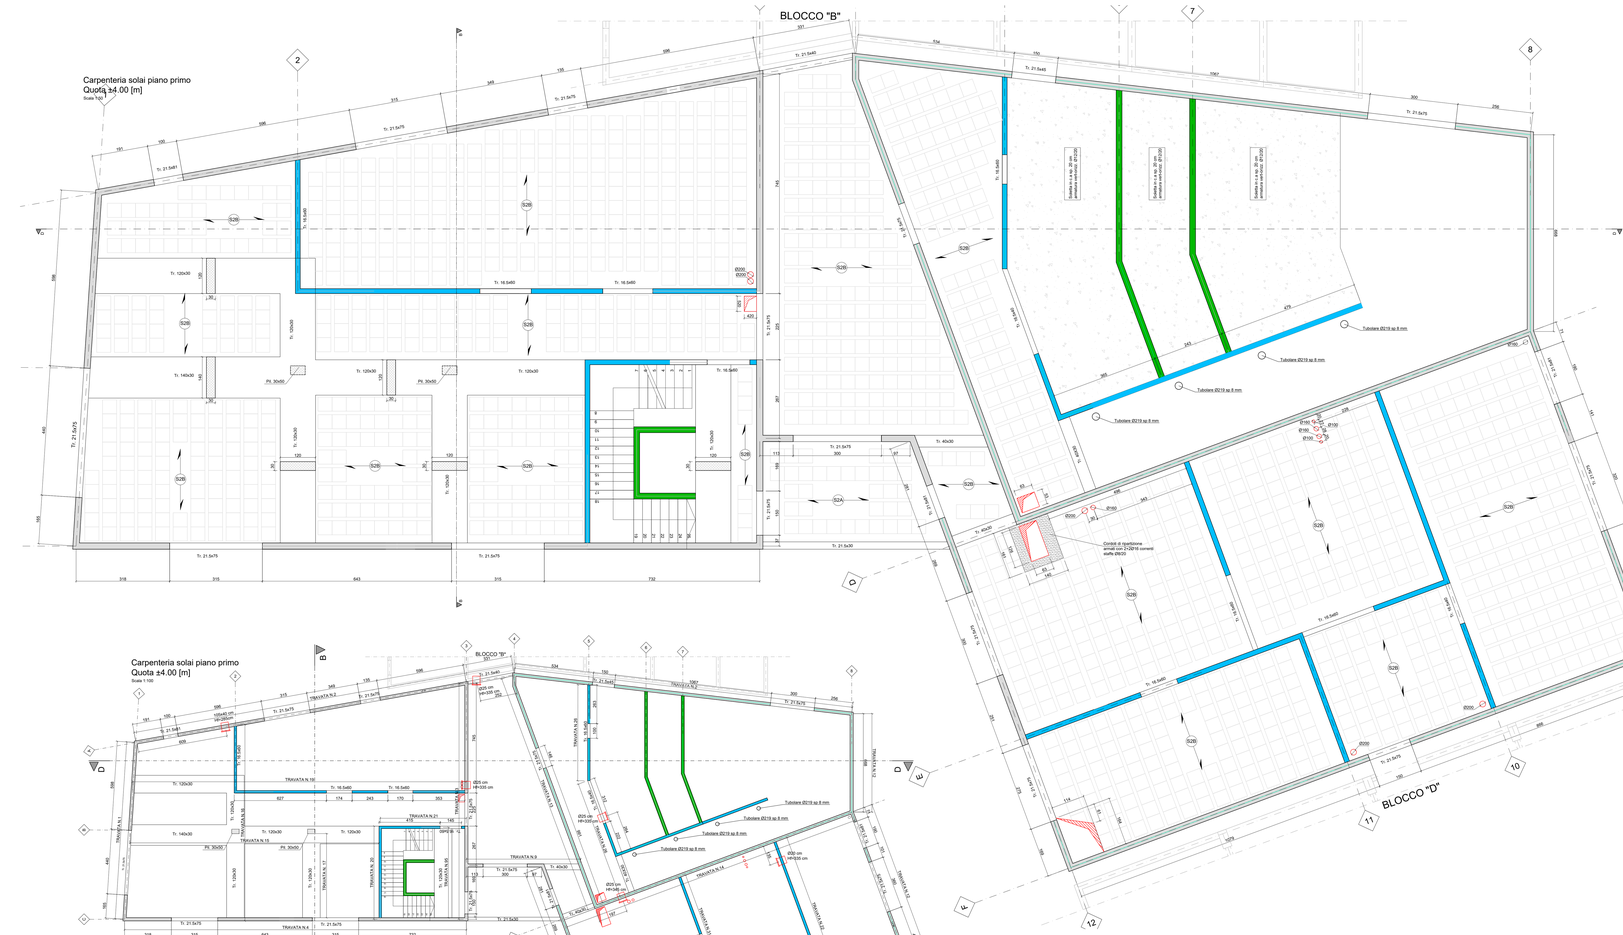
BLOCCO "B"
BLOCCO "D"
Carpenteria solai piano primo
Quota ±4.00 [m]
Scala 1:100
Tr. 21.5x75
Tr. 21.5x40
Tr. 21.5x50
Tr. 16.5x60
Tr. 120x30
Tr. 140x30
Tr. 145x30
Tr. 130x30
Pil. 30x50
Tr. 45x30
Tubolare Ø219 sp.8 mm
Tubolare Ø219 sp.6 mm
Tubolare Ø219 sp.5 mm
Tubolare Ø219 sp.4 mm
Tubolare Ø219 sp.3 mm
Colonne Ø300
Colonne Ø350
Ø25 cm HH:335 cm
Ø20 cm HH:335 cm
40x90 cm HH:22 cm
Ø20 cm HH:335 cm
Cordoli di ripartizione armati con 2+2Ø16 correnti staffe Ø8/20
TRAVATA N.1
TRAVATA N.2
TRAVATA N.3
TRAVATA N.4
TRAVATA N.5
TRAVATA N.6
TRAVATA N.7
TRAVATA N.8
TRAVATA N.9
TRAVATA N.10
TRAVATA N.11
TRAVATA N.12
TRAVATA N.13
TRAVATA N.14
TRAVATA N.15
TRAVATA N.16
TRAVATA N.17
TRAVATA N.18
TRAVATA N.19
TRAVATA N.20
TRAVATA